
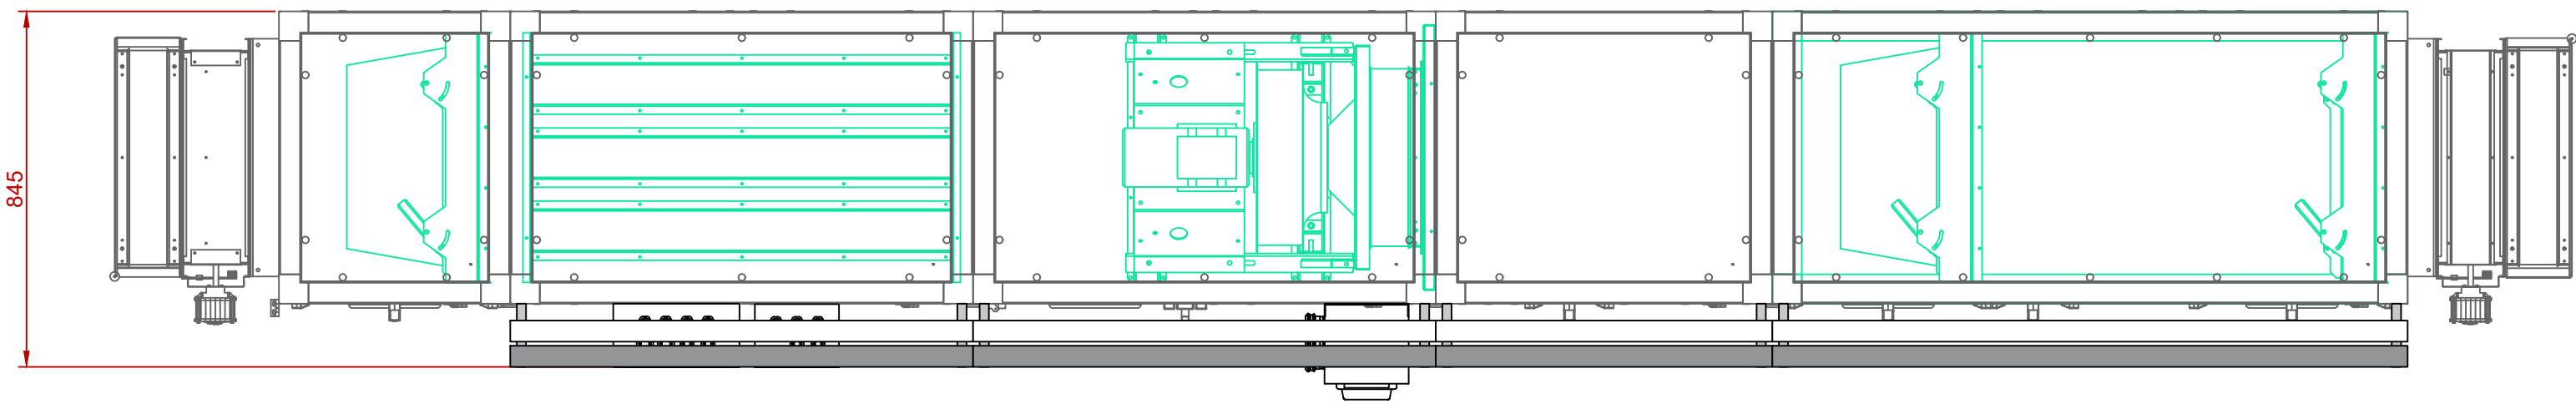


24104
20/авг 14:20

Чертёж с расположением коробок и оборудования КИПиА
ВЦК "Сахара-С"-П-45 (δ/з 24104)
Вид со стороны обслуживания
8315-B02-AH-001A, 8315-B02-AH-001B

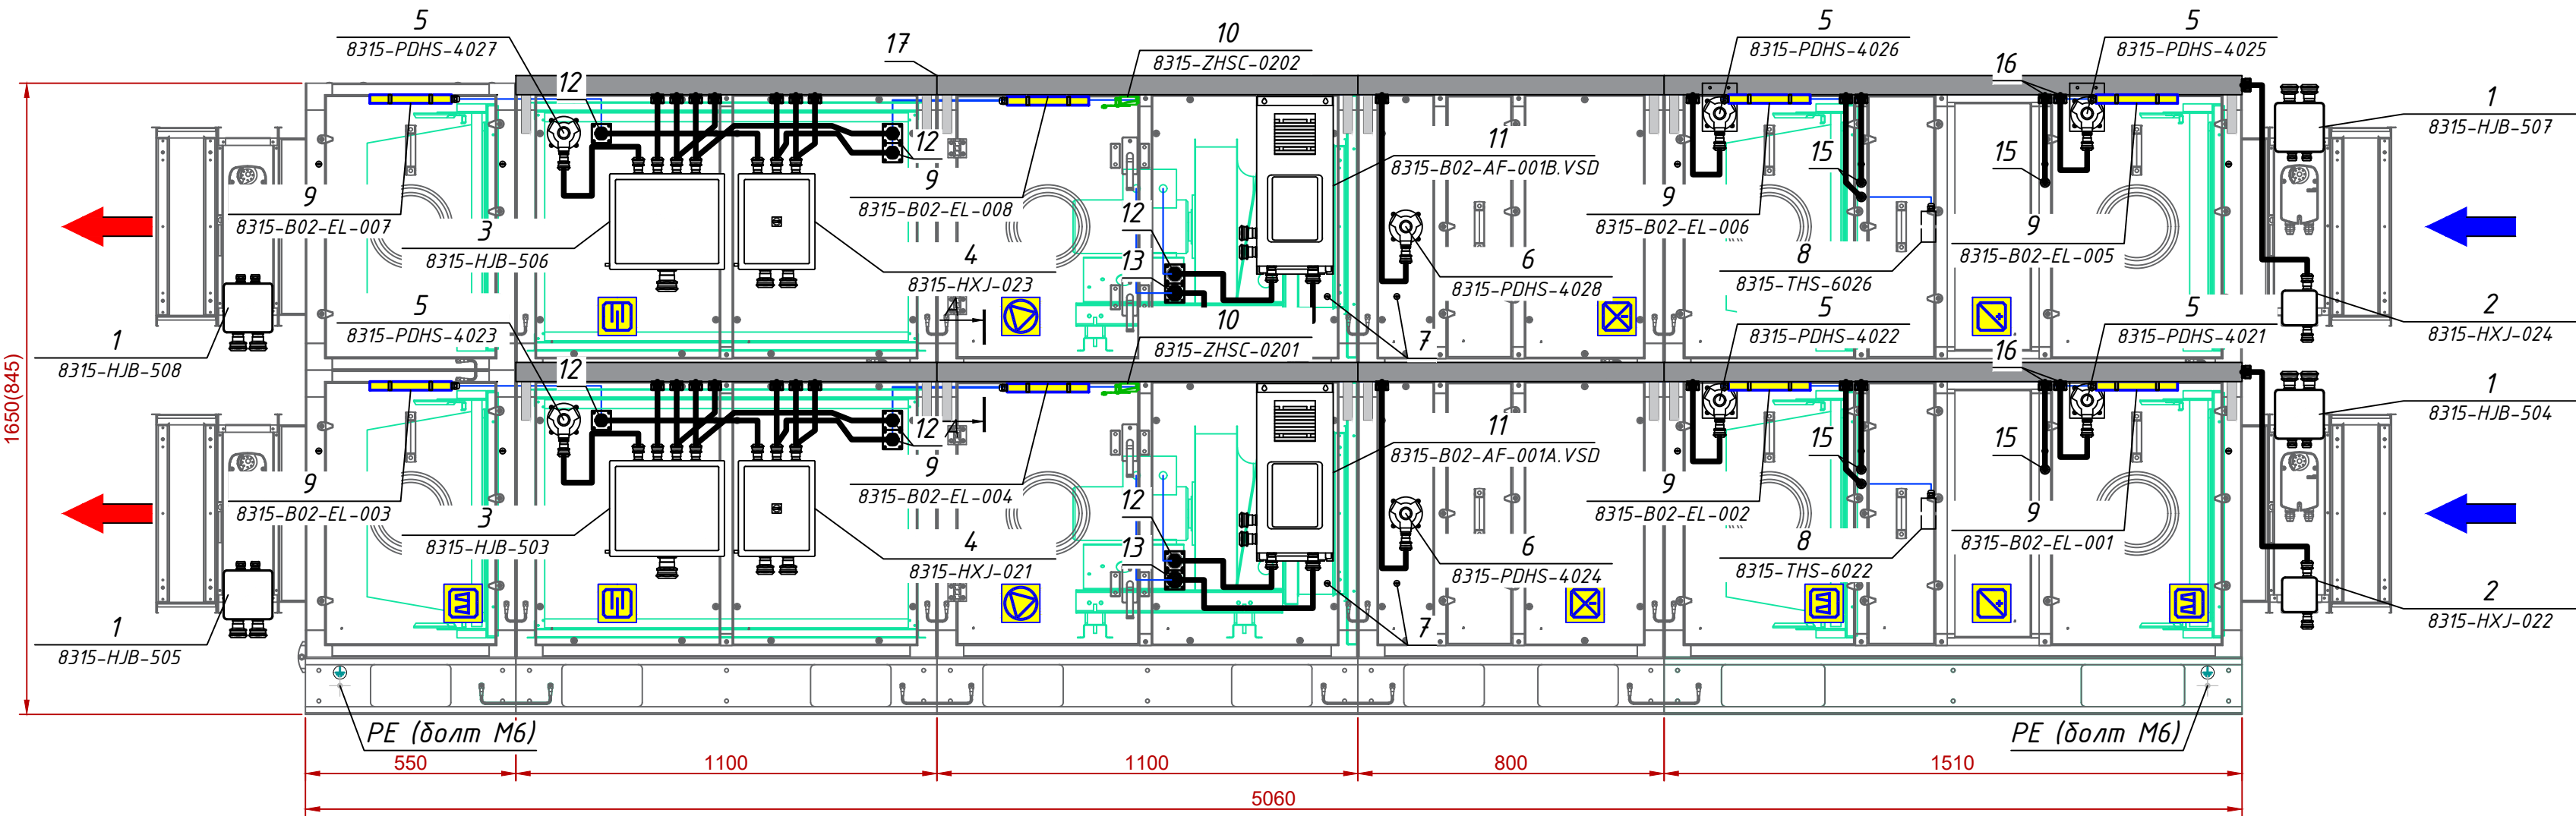

ВНИМАНИЕ!


Установить кабельные вводы в ЧРП (VF-101 5,5кВт):

- Питание ЧРП - 20АК Ni (Dk=6,5-13,9, Dkδ=12,5-20,9) ATELEX
- Питание ЭД - ВК-M20-16-MP20 Dk=8-16 ZETA
- PTC термистор - ВК-M20-12-MP15 Dk=6-12 ZETA
- Modbus - ВК-M20-16-MP20 Dk=8-16 ZETA
- Modbus - ВК-M20-16-MP20 Dk=8-16 ZETA
- Пуск/авария - ВК-M20-16-MP20 Dk=8-16 ZETA

Установить кабельные вводы в БРНО ЭД:

- питание ЭД - M20x1,5 Dk=6-12 Ferrol
- PTC термистор - M20x1,5 Dk=6-12 Ferrol

A - A

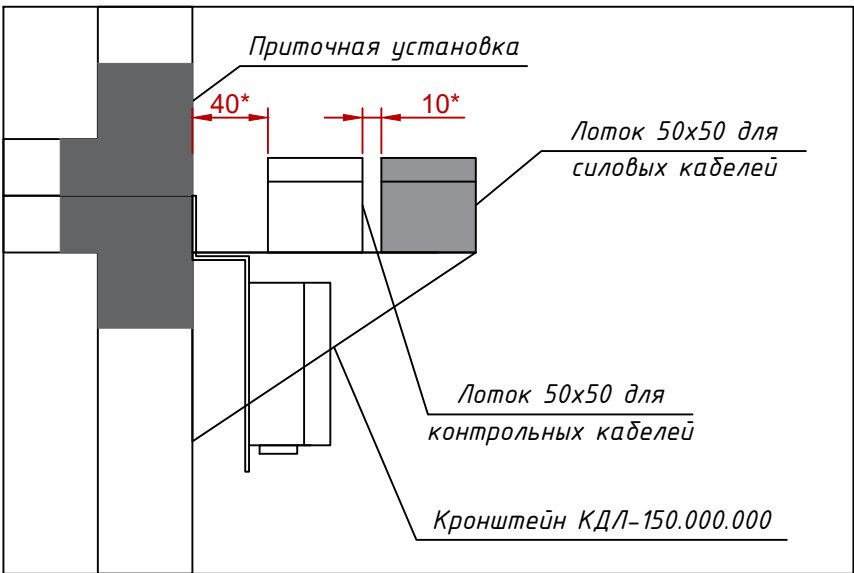

- 2 Капиллярные термостаты от замораживания по воздуху устанавливаются на заводе изготовителе внутри ВЦК.
- 3 Проходы через сэндвич-панели выполнять по принципу - сальник ступенчатый внутри, кабельный ввод снаружи приточной системы.
- 4 Расположение коробок, датчиков КИПиА носит рекомендательный характер и может быть изменено в процессе проектирования и электромонтажа.
- 5 Места расположения кабельных вводов в коробке несут рекомендательный характер и могут быть изменены в зависимости от места установки коробки.
- 6 Выполнить заземление электродвигателей проводом ПуГВж/з 6 мм2. При отсутствии болта заземления просверлить отверстие в электродвигателе и закрепить заземление при помощи болта.
- 7 На клеммные коробки двигателя, обогрева воздушных клапанов наклеить наклейки: "Открывать отключив от сети" и (W08) "Внимание электрическое напряжение".



* Размеры для справки
1 Оборудование КИП входит в монтажный комплект и устанавливается силами заказчика на объекте, на ВЦК установить кронштейны.

					ВЦК "Сахара-С"-П-45 (δ/з 24104)							
					Амурский газохимический комплекс (ГХК). 8315			Лит.		Масса	Масштаб	
Изм.	Лист	Ндокум.	Подп.	Дата								
Разраб.	Арестов	КЗ	29.07.2026									
Пров.	Говоров	ГЗ	29.07.2026									
								Лист. 1		Листов		
Н.контр.					Чертёж с расположением коробок и оборудования КИПиА			000 "Феррум"				
Утв.	Круницын	КЗ	29.07.2026									

Поз. обознач.	Наименование	Кол-во	Примечание	Поз. обознач.	Наименование	Кол-во	Примечание
1	Коробка клеммная для питания и управления ЭП клапана, в составе:	–	см.лист 2	2	Коробка клеммная для питания обогрева клапана, в составе:	–	см.лист 2
1.1	Коробка распределительная HENSEL KF 0600 G 130x130x77	1		2.1	Коробка распределительная HENSEL KF 0200 G 93x93x62	1	
1.2	Din-рейка металл. перф. 15x5,5 мм	0,1	м	2.2	Din-рейка металл. перф. 15x5,5 мм	0,1	м
1.3	Проходная мини-клемма WS2.5-DIN15-01P-11-00A(H) DEGSON	8		2.3	Проходная мини-клемма WS2.5-DIN15-01P-11-00A(H) DEGSON	3	
1.4	Концевая крышка D-WS2.5-MID-CO-01P-11-00A(H) DEGSON	1		2.4	Концевая крышка D-WS2.5-MID-CO-01P-11-00A(H) DEGSON	1	
1.5	Каб. ввод Ferrrol ник.латунь M20x1.5	2		2.5	Каб.ввод под металлорукав ВК-M20-12-MP15, IP67,ник.лат.	2	
1.6	Каб.ввод под металлорукав ВК-M25-18-MP25, IP67,ник.лат.	2	Для заказчика				



Коробка клеммная для питания и управления ЭП клапана
(поз. 1)

Коробка клеммная для питания обогрева клапана
(поз. 2)

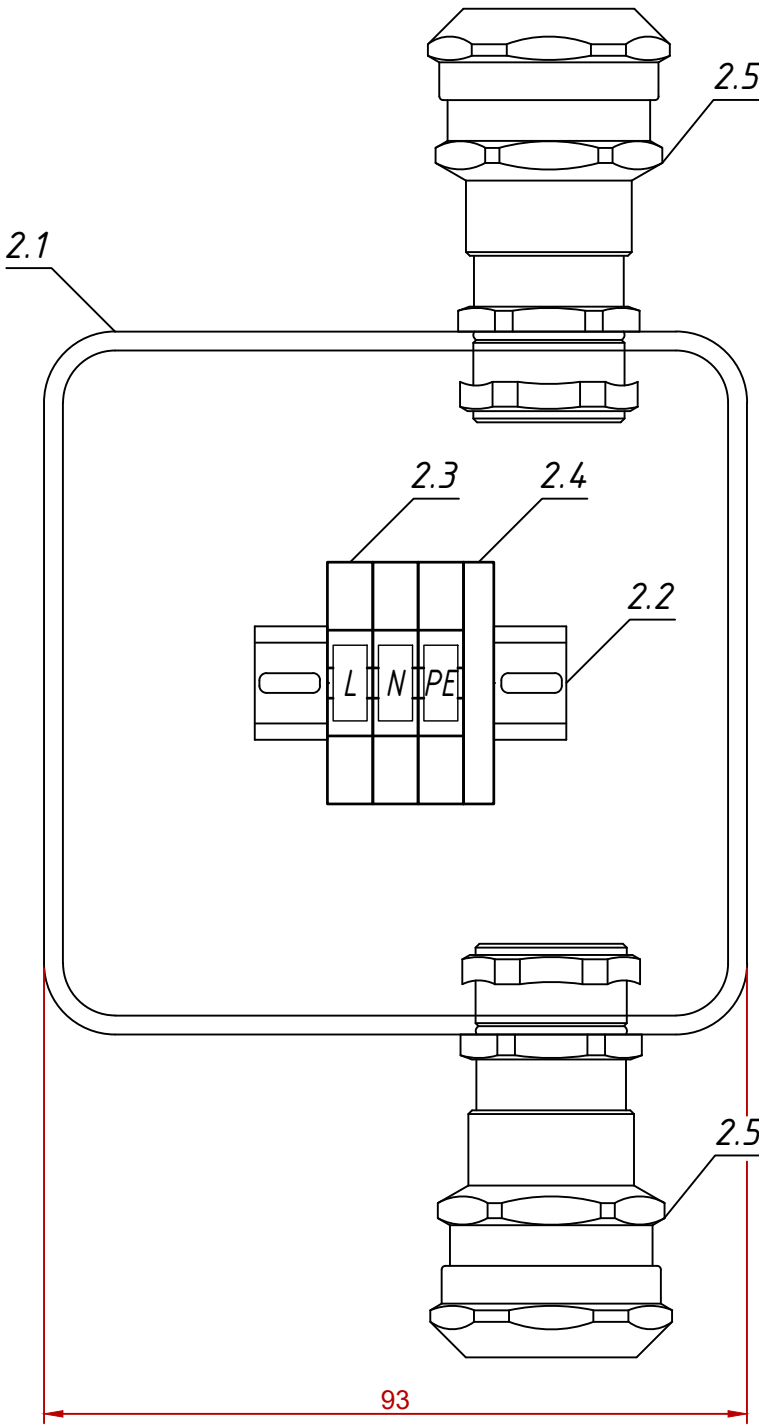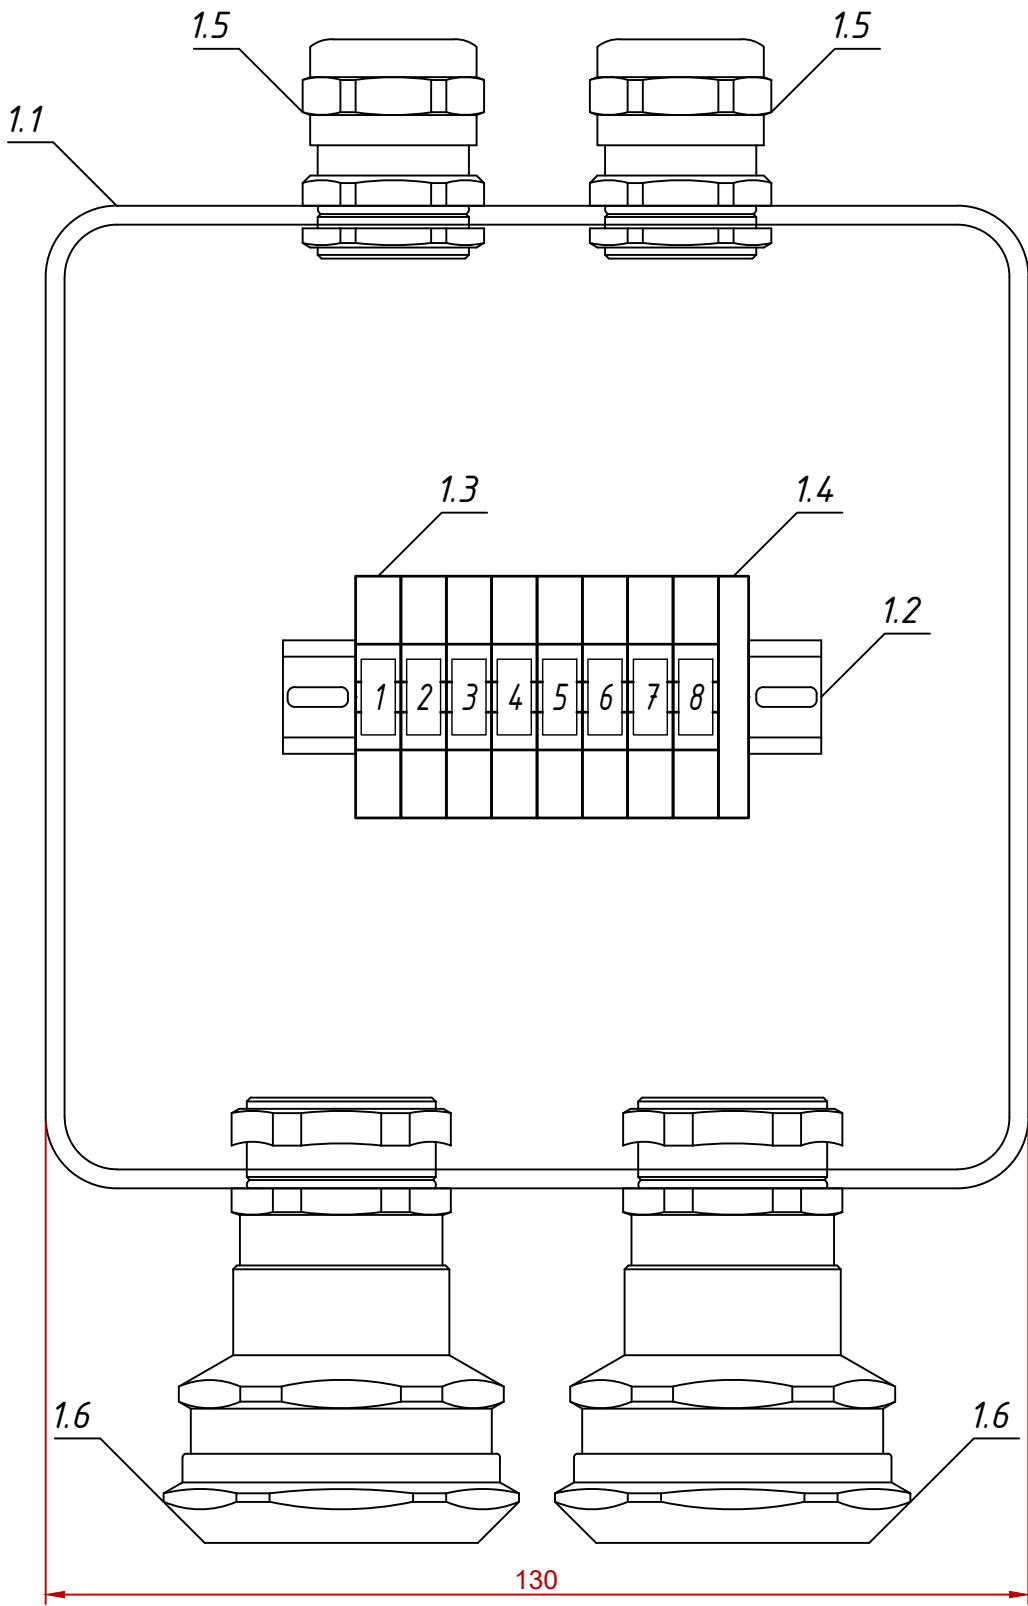



Коробка клеммная общая для контрольных кабелей
(поз. 3)

Поз. обознач.	Наименование	Кол-во	Примечание
3	Коробка клеммная общая для контрольных кабелей, в составе:	–	см. лист 2
3.1	МНК-250Х300Х150-0-RAL9006-3	1	
3.2	Dip-рейка металл. перф. 35х7,5 мм	0,25	м
3.3	Клемма пружинная КПИ 2В-2,5 31А (серий) IEK	31	
3.4	Заглушка для клеммы КПИ 2В-1,5/2,5 (серий) IEK	1	
3.5	Ограничитель на Dip-рейку 35 мм металл.	2	
3.6	Каб.ввод под металлорукав ВК-М20-12-МР15, IP67,ник.лат.	6	
3.7	Каб.ввод под металлорукав ВК-М20-16-МР20, IP67,ник.лат.	2	Для заказчика
3.8	Каб.ввод под металлорукав ВК-М40-25-МР32, IP67,ник.лат.	1	Для заказчика
3.9	Кабельный канал – СД 40Х60	0,5	м


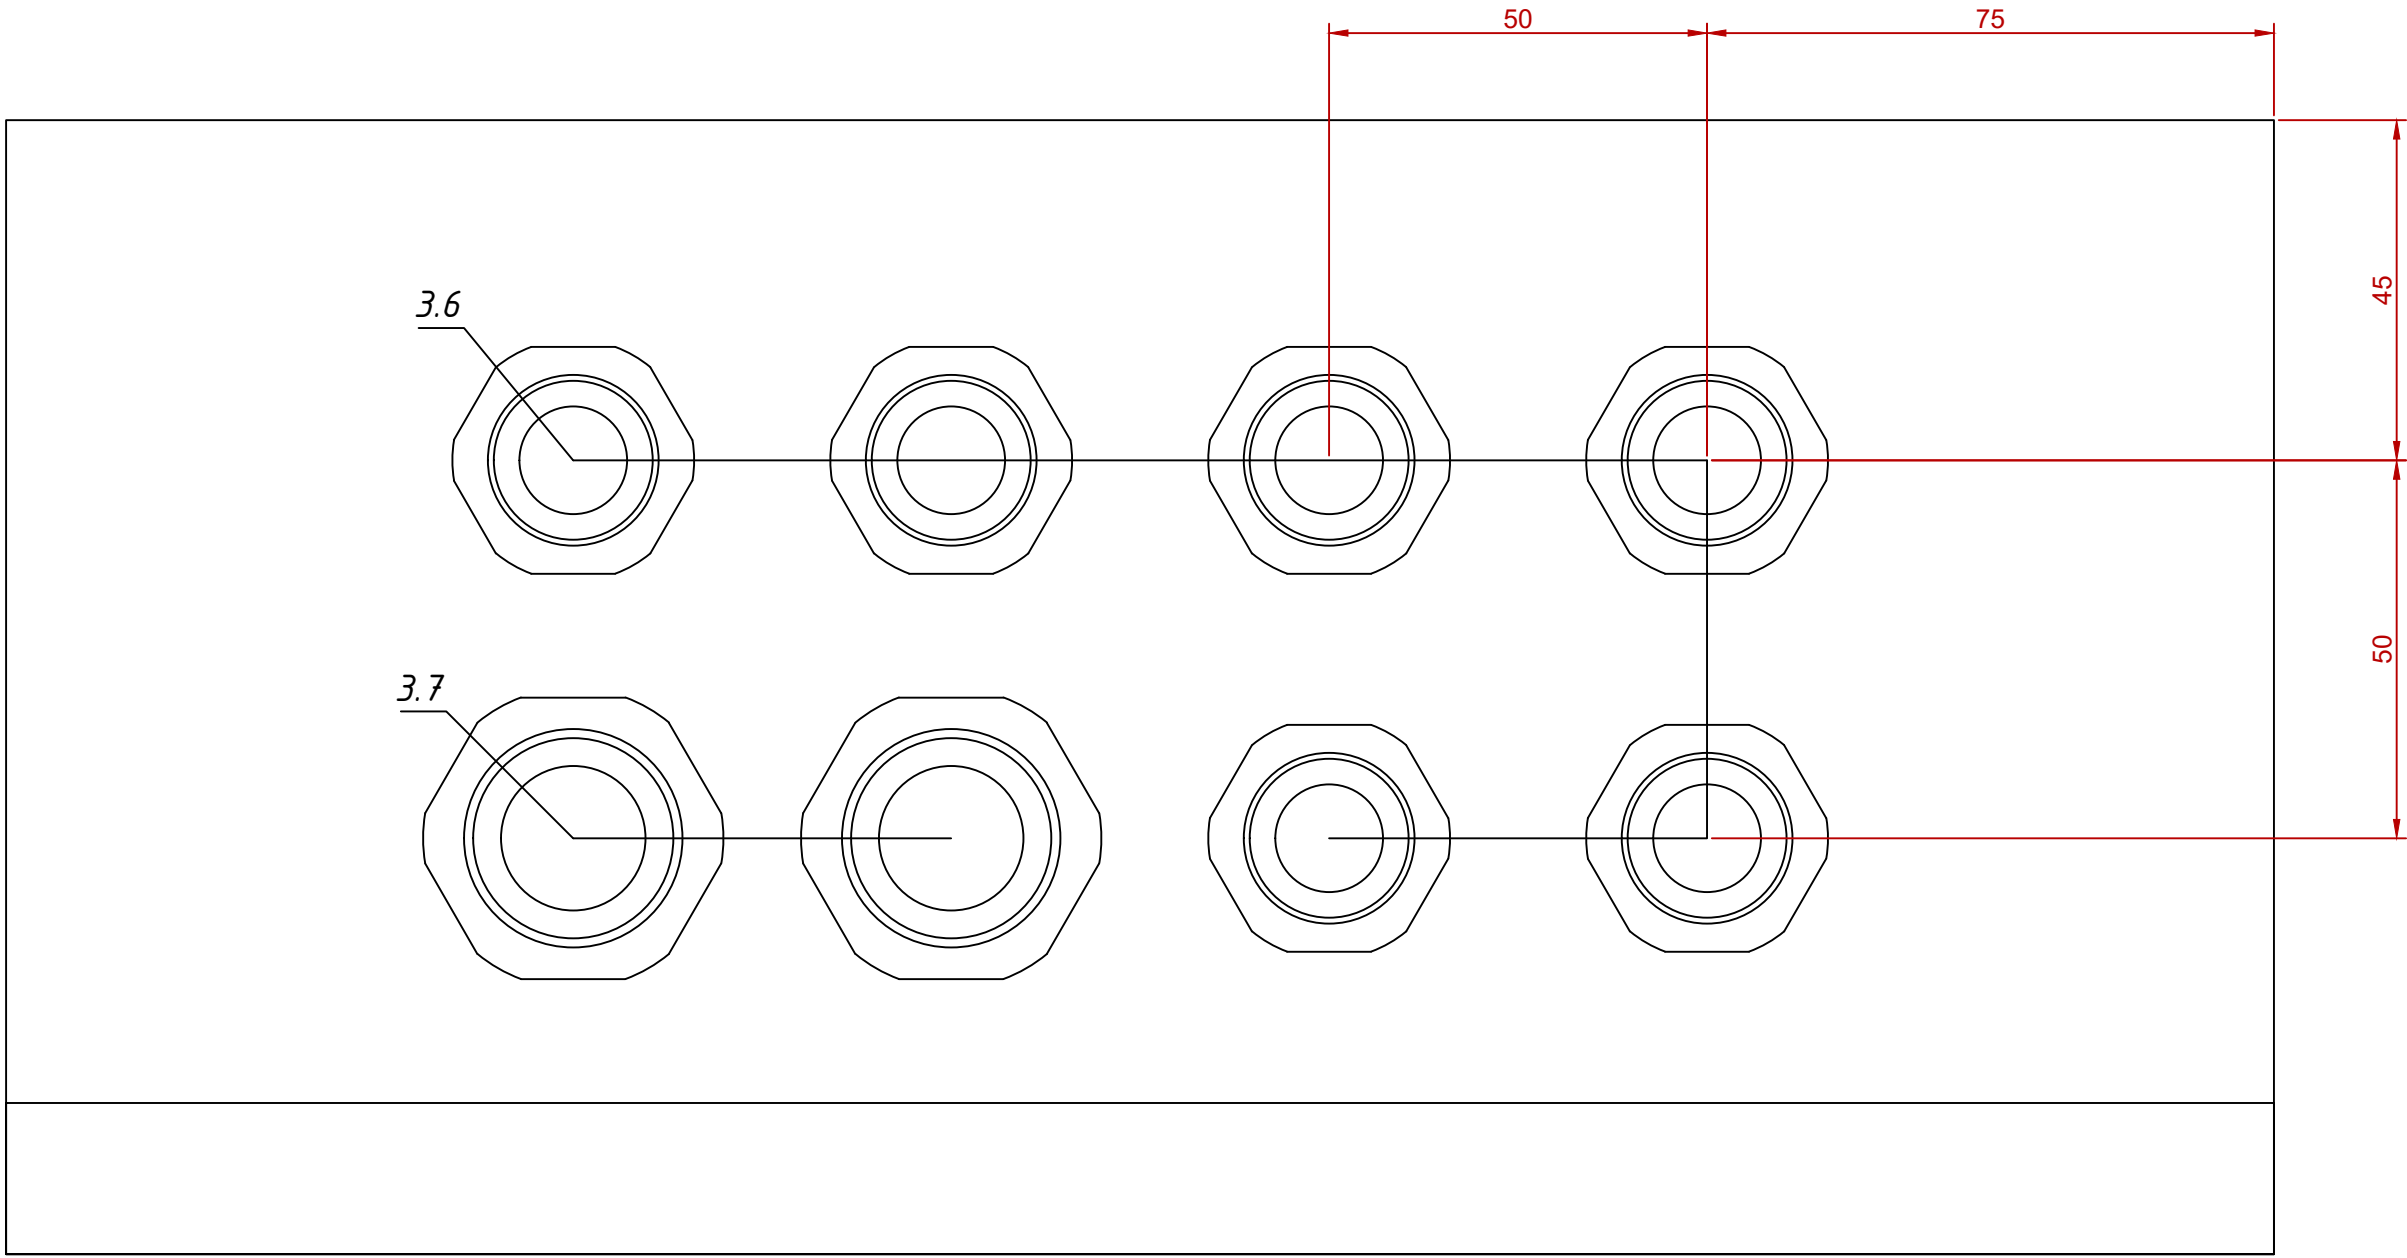
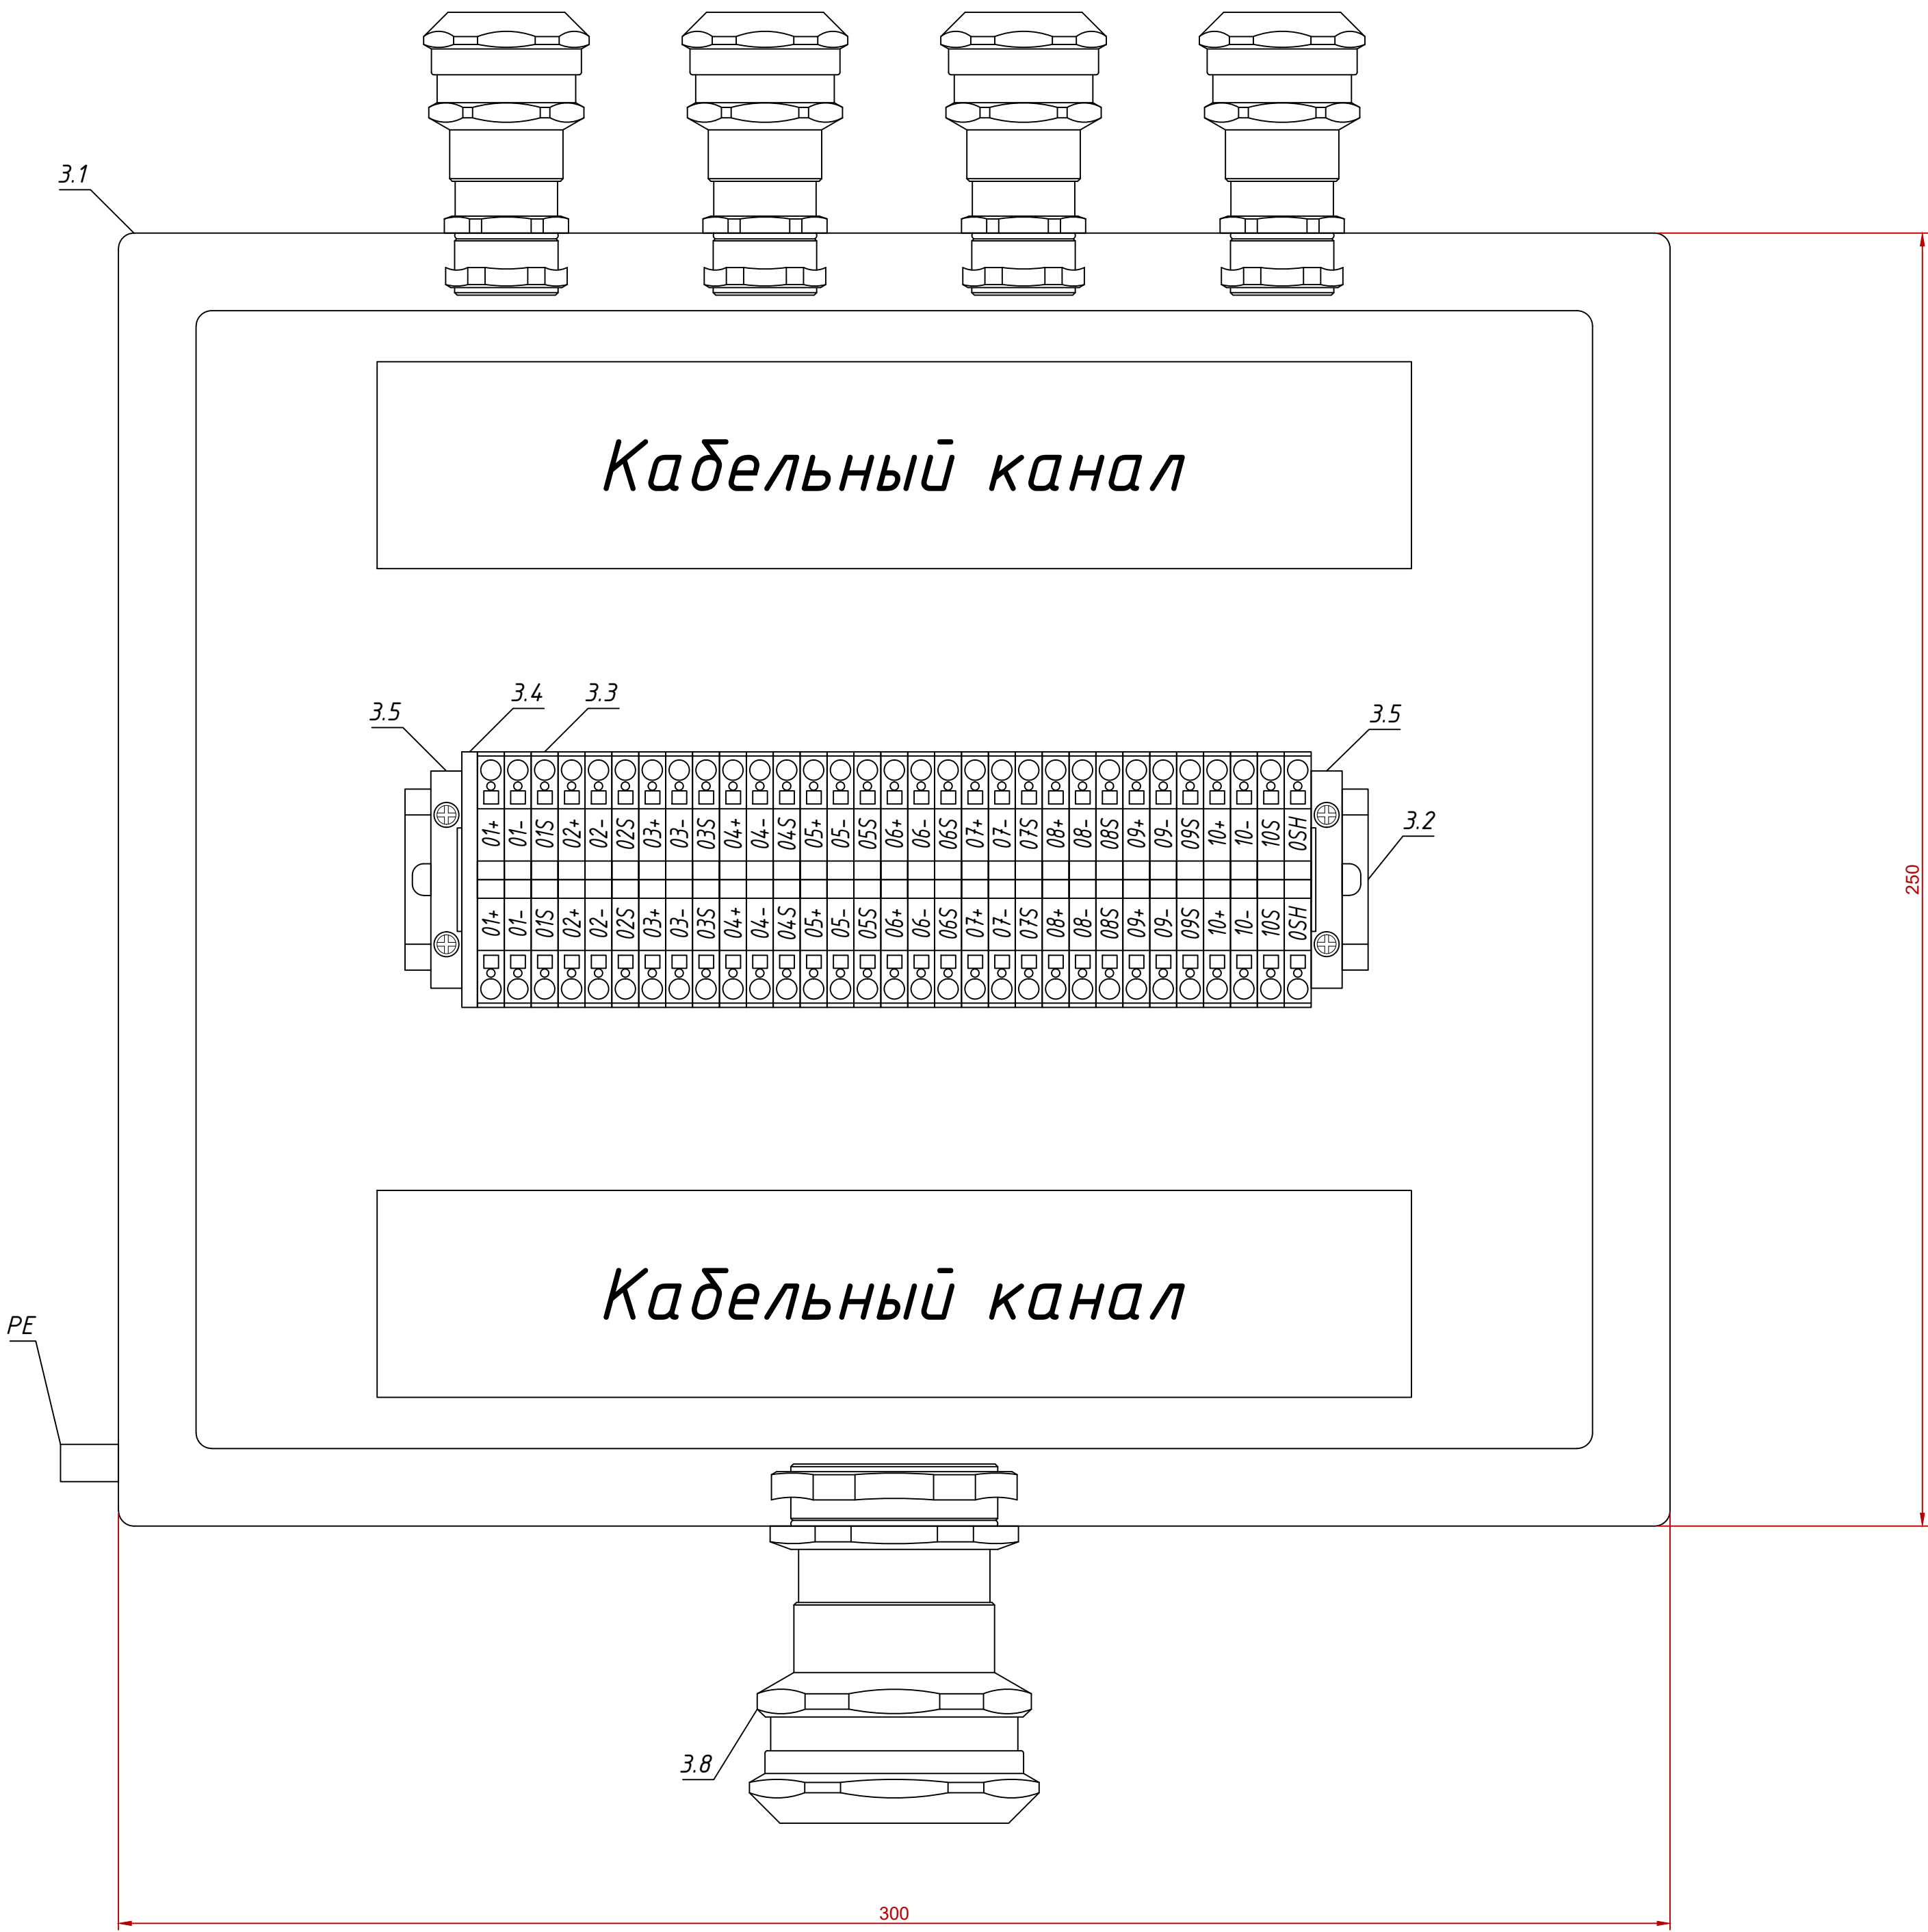




Коробка клеммная общая для силовых кабелей
(поз. 4)

Поз. обознач.	Наименование	Кол-во	Примечание
4	Коробка клеммная общая для силовых кабелей, в составе:	–	см.лист 2
4.1	МНК-250Х200Х150-0-RAL9006-4	1	
4.2	Dip-рейка металл. перф. 35х7,5 мм	0,2	м
4.3	Клемма пружинная КПИ 2В-2,5 31А (серый) IEK	16	
4.4	Заглушка для клеммы КПИ 2В-1,5/2,5 (серый) IEK	1	
4.5	Ограничитель на Dip-рейку 35 мм металл.	2	
4.6	Каб.ввод под металлорукав ВК-М20-12-МР15, IP67,ник.лат.	5	
4.7	Каб.ввод под металлорукав ВК-М25-18-МР25, IP67,ник.лат.	2	Для заказчика
4.8	Кабельный канал – CD 40Х60	0,4	м
4.9	Переключатель SB5 в сборе модульный 22 мм, 1НО	1	Установить доп. блок
	Блок контактный 1 НО (SBE101) Systeme Electric	1	

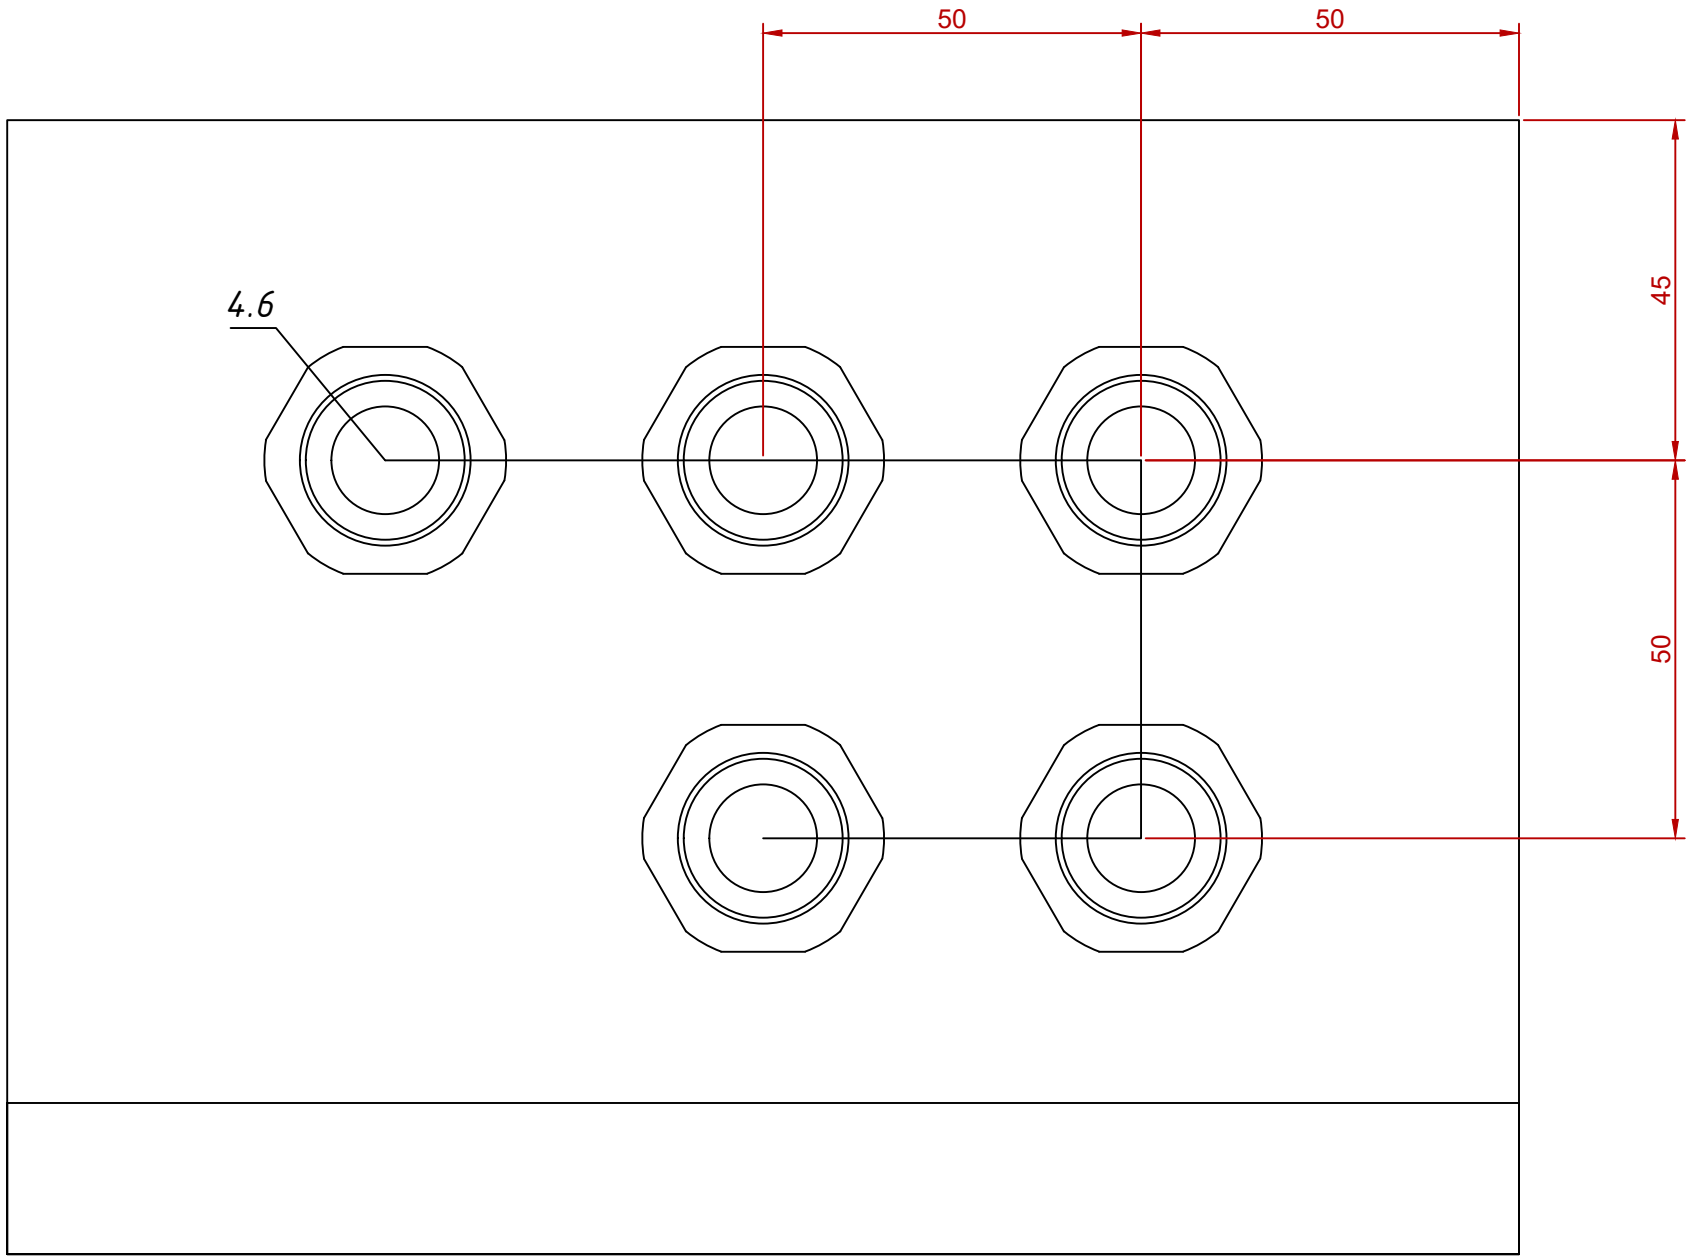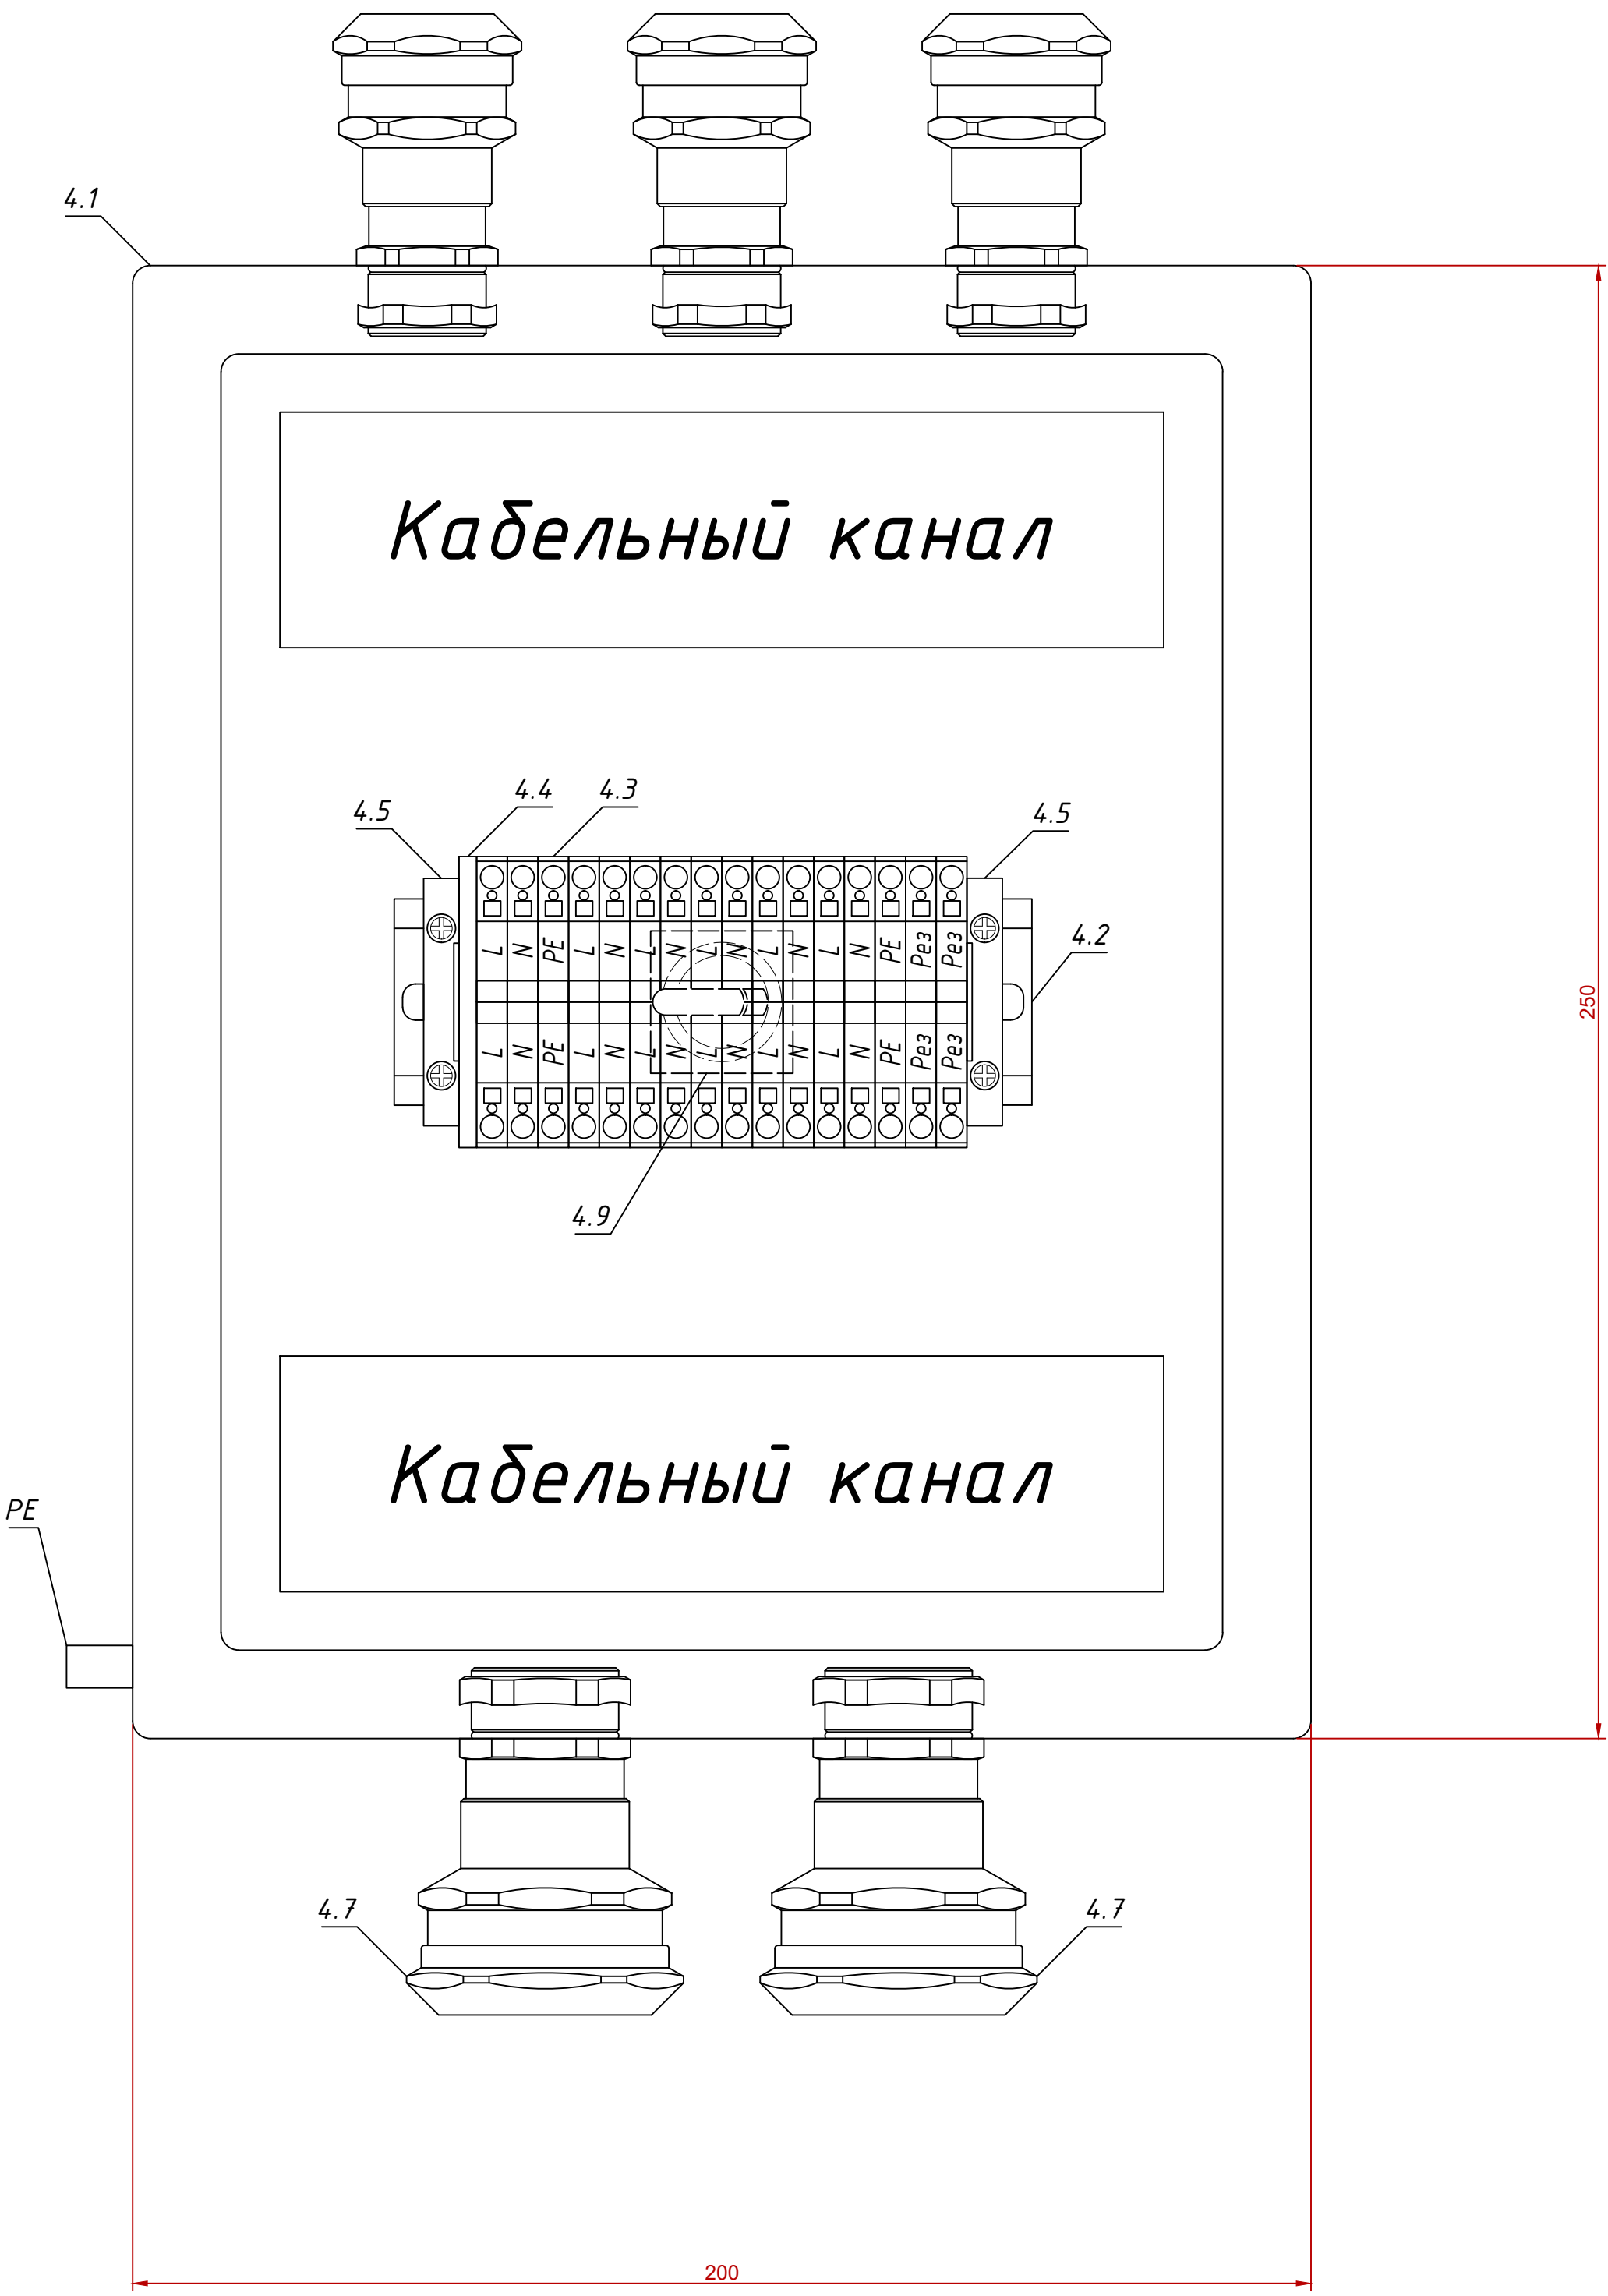

Инв. N подл.	Подпись и дата	Взам. инв. N

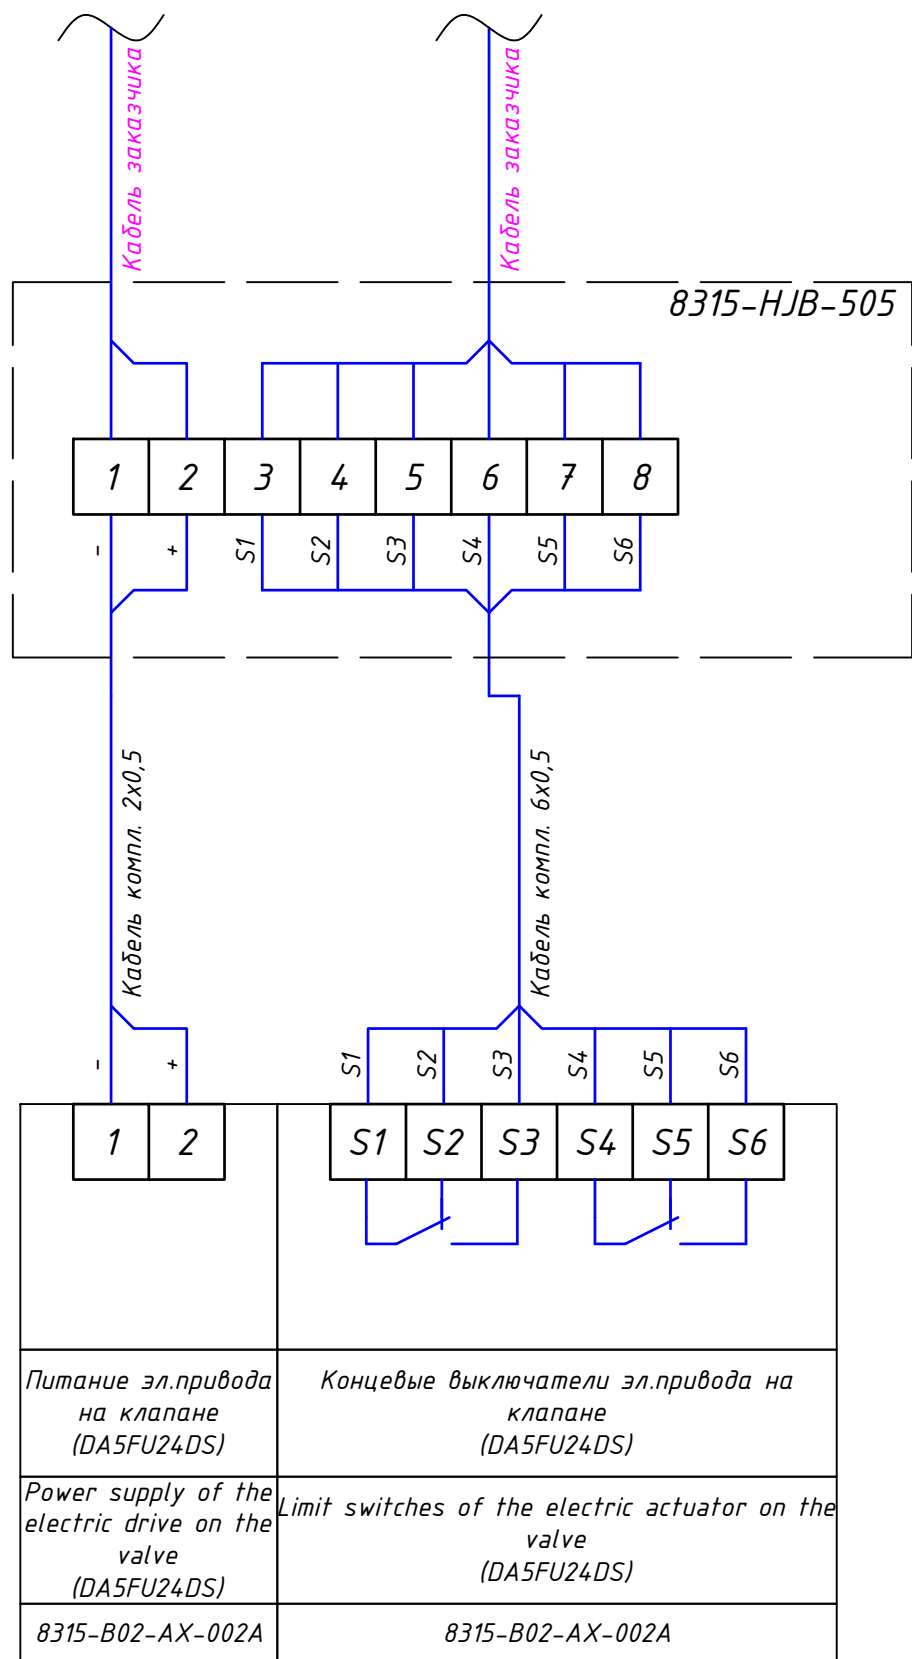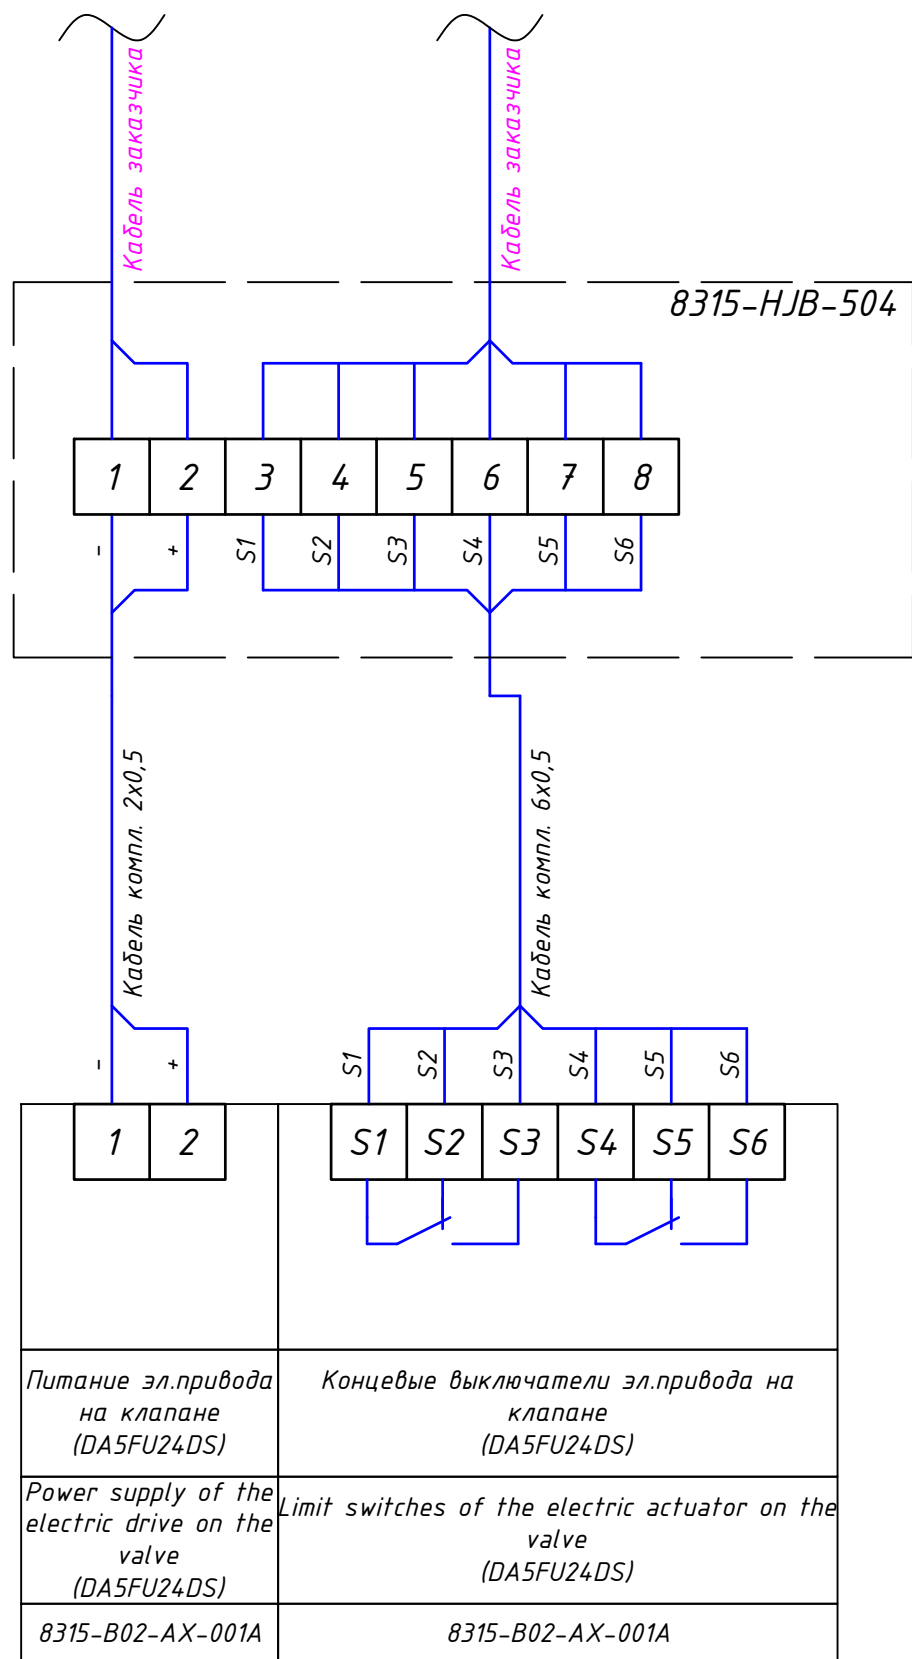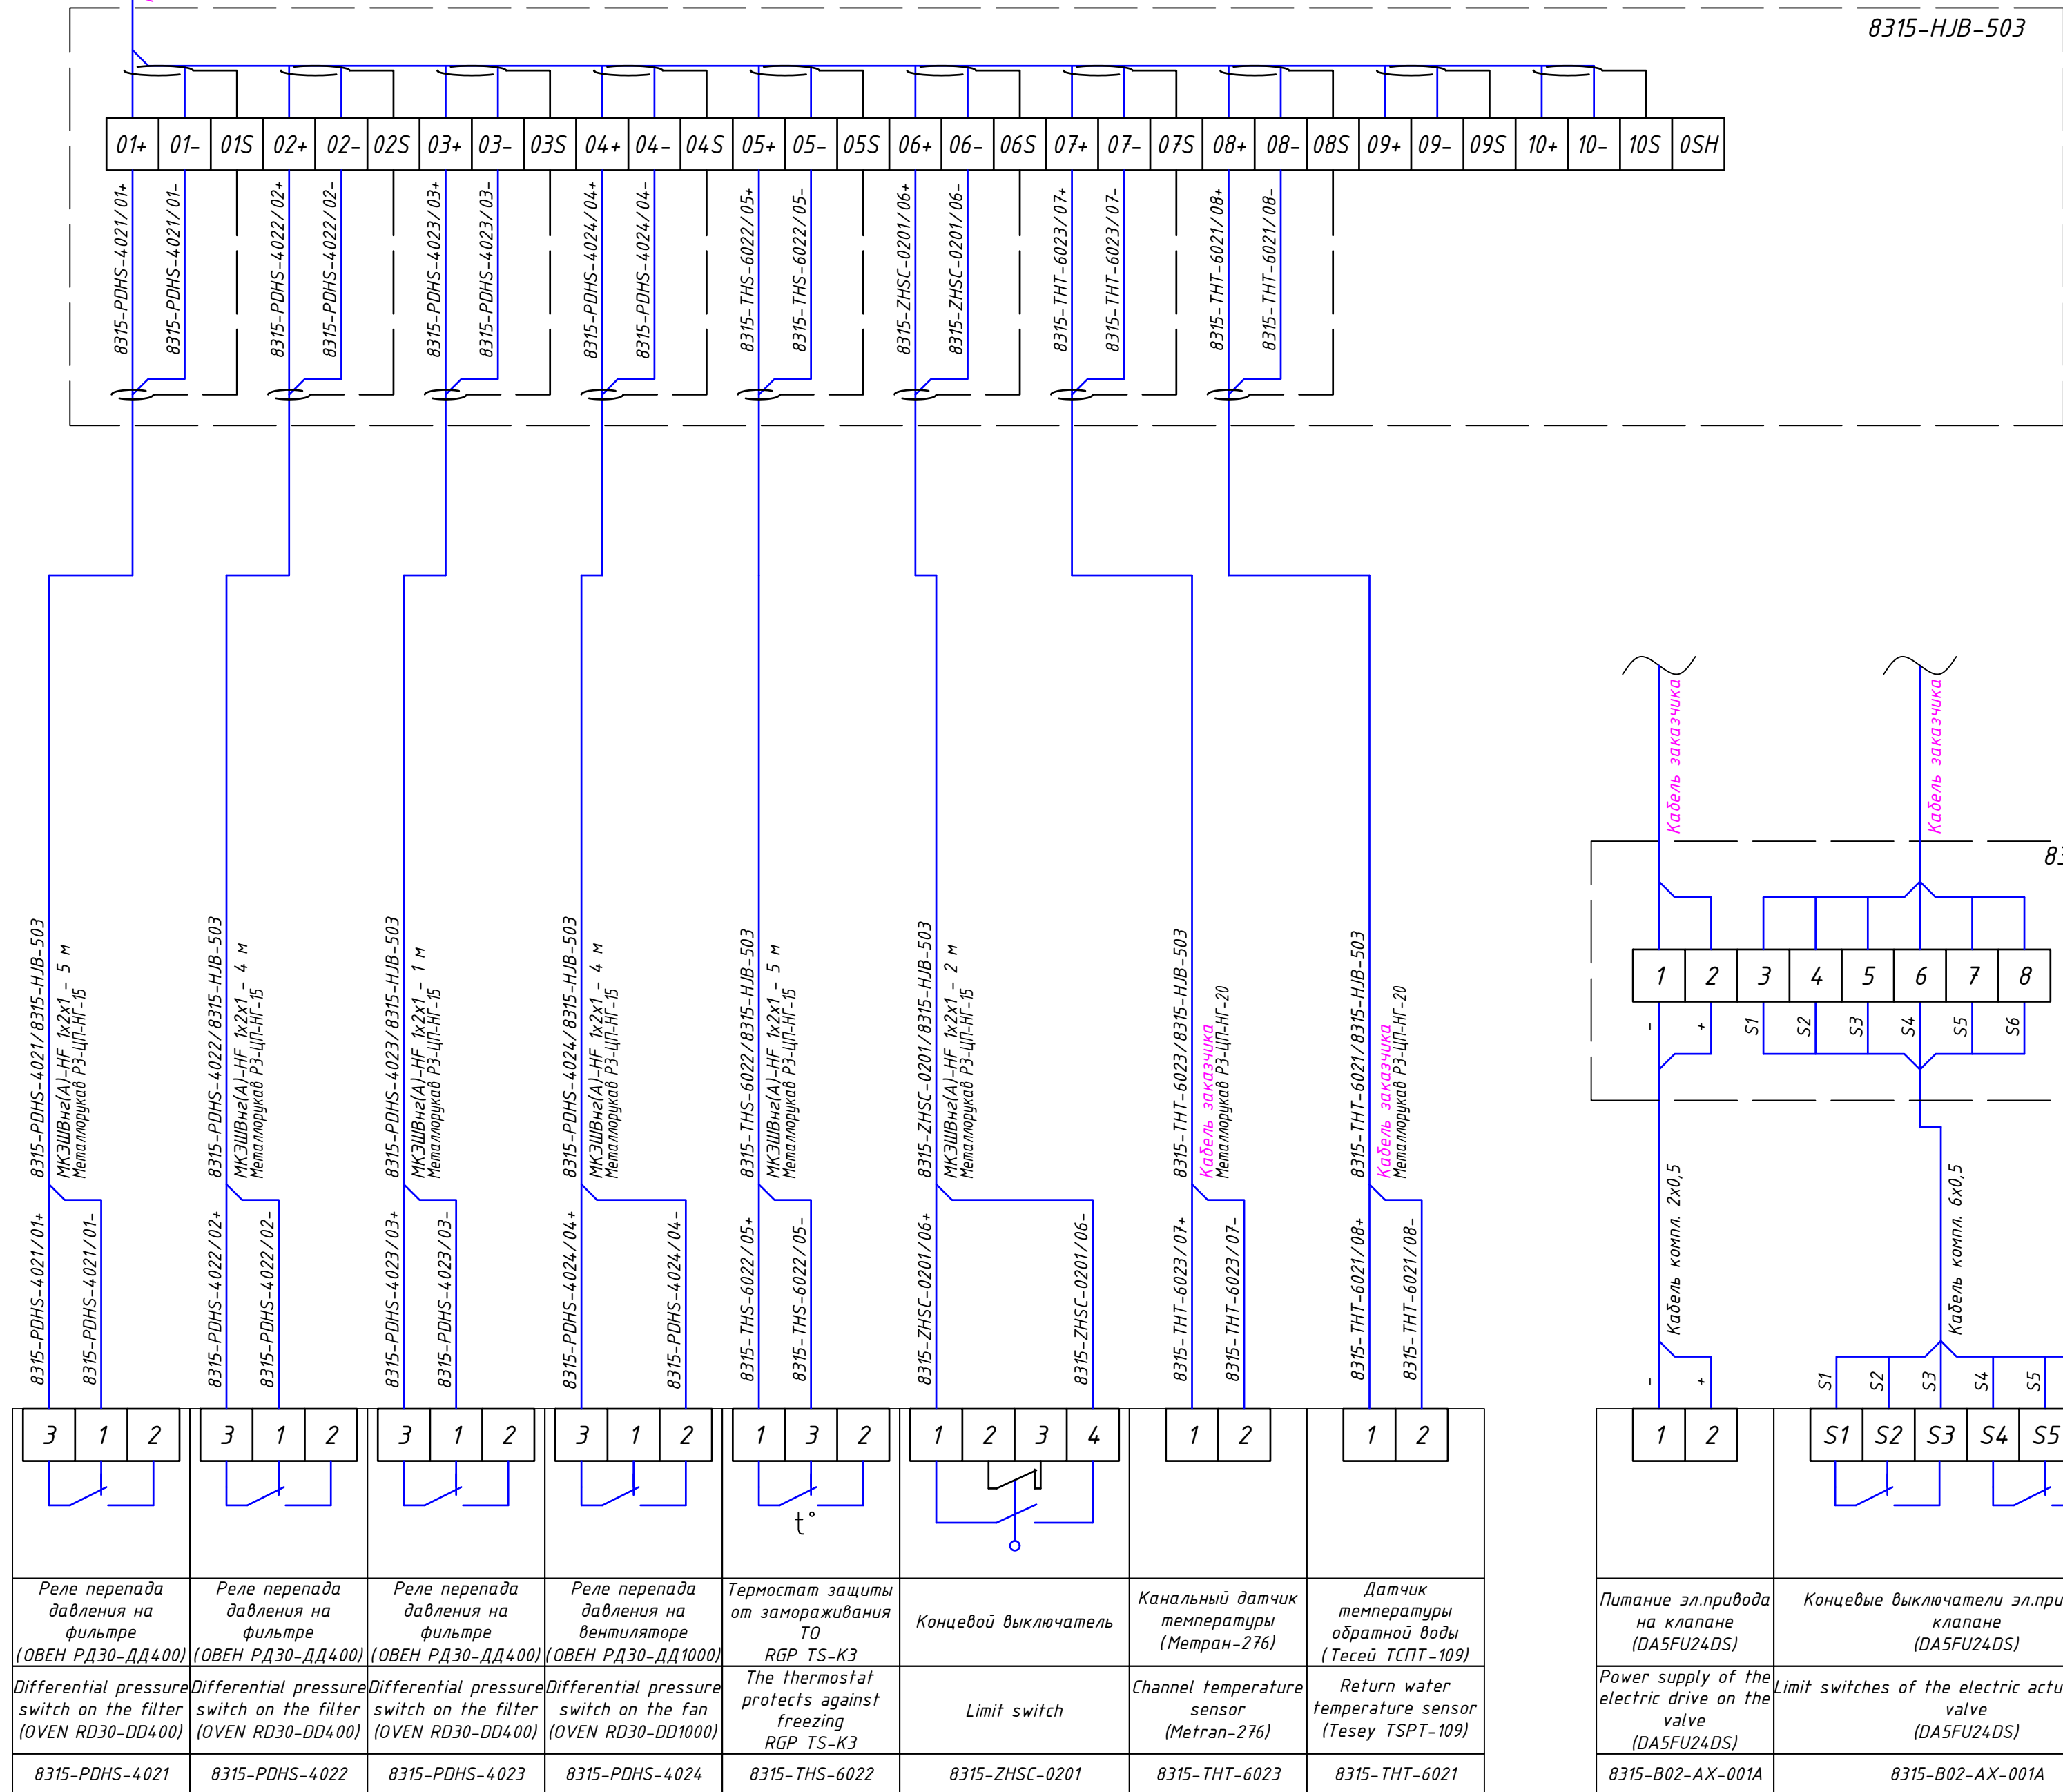


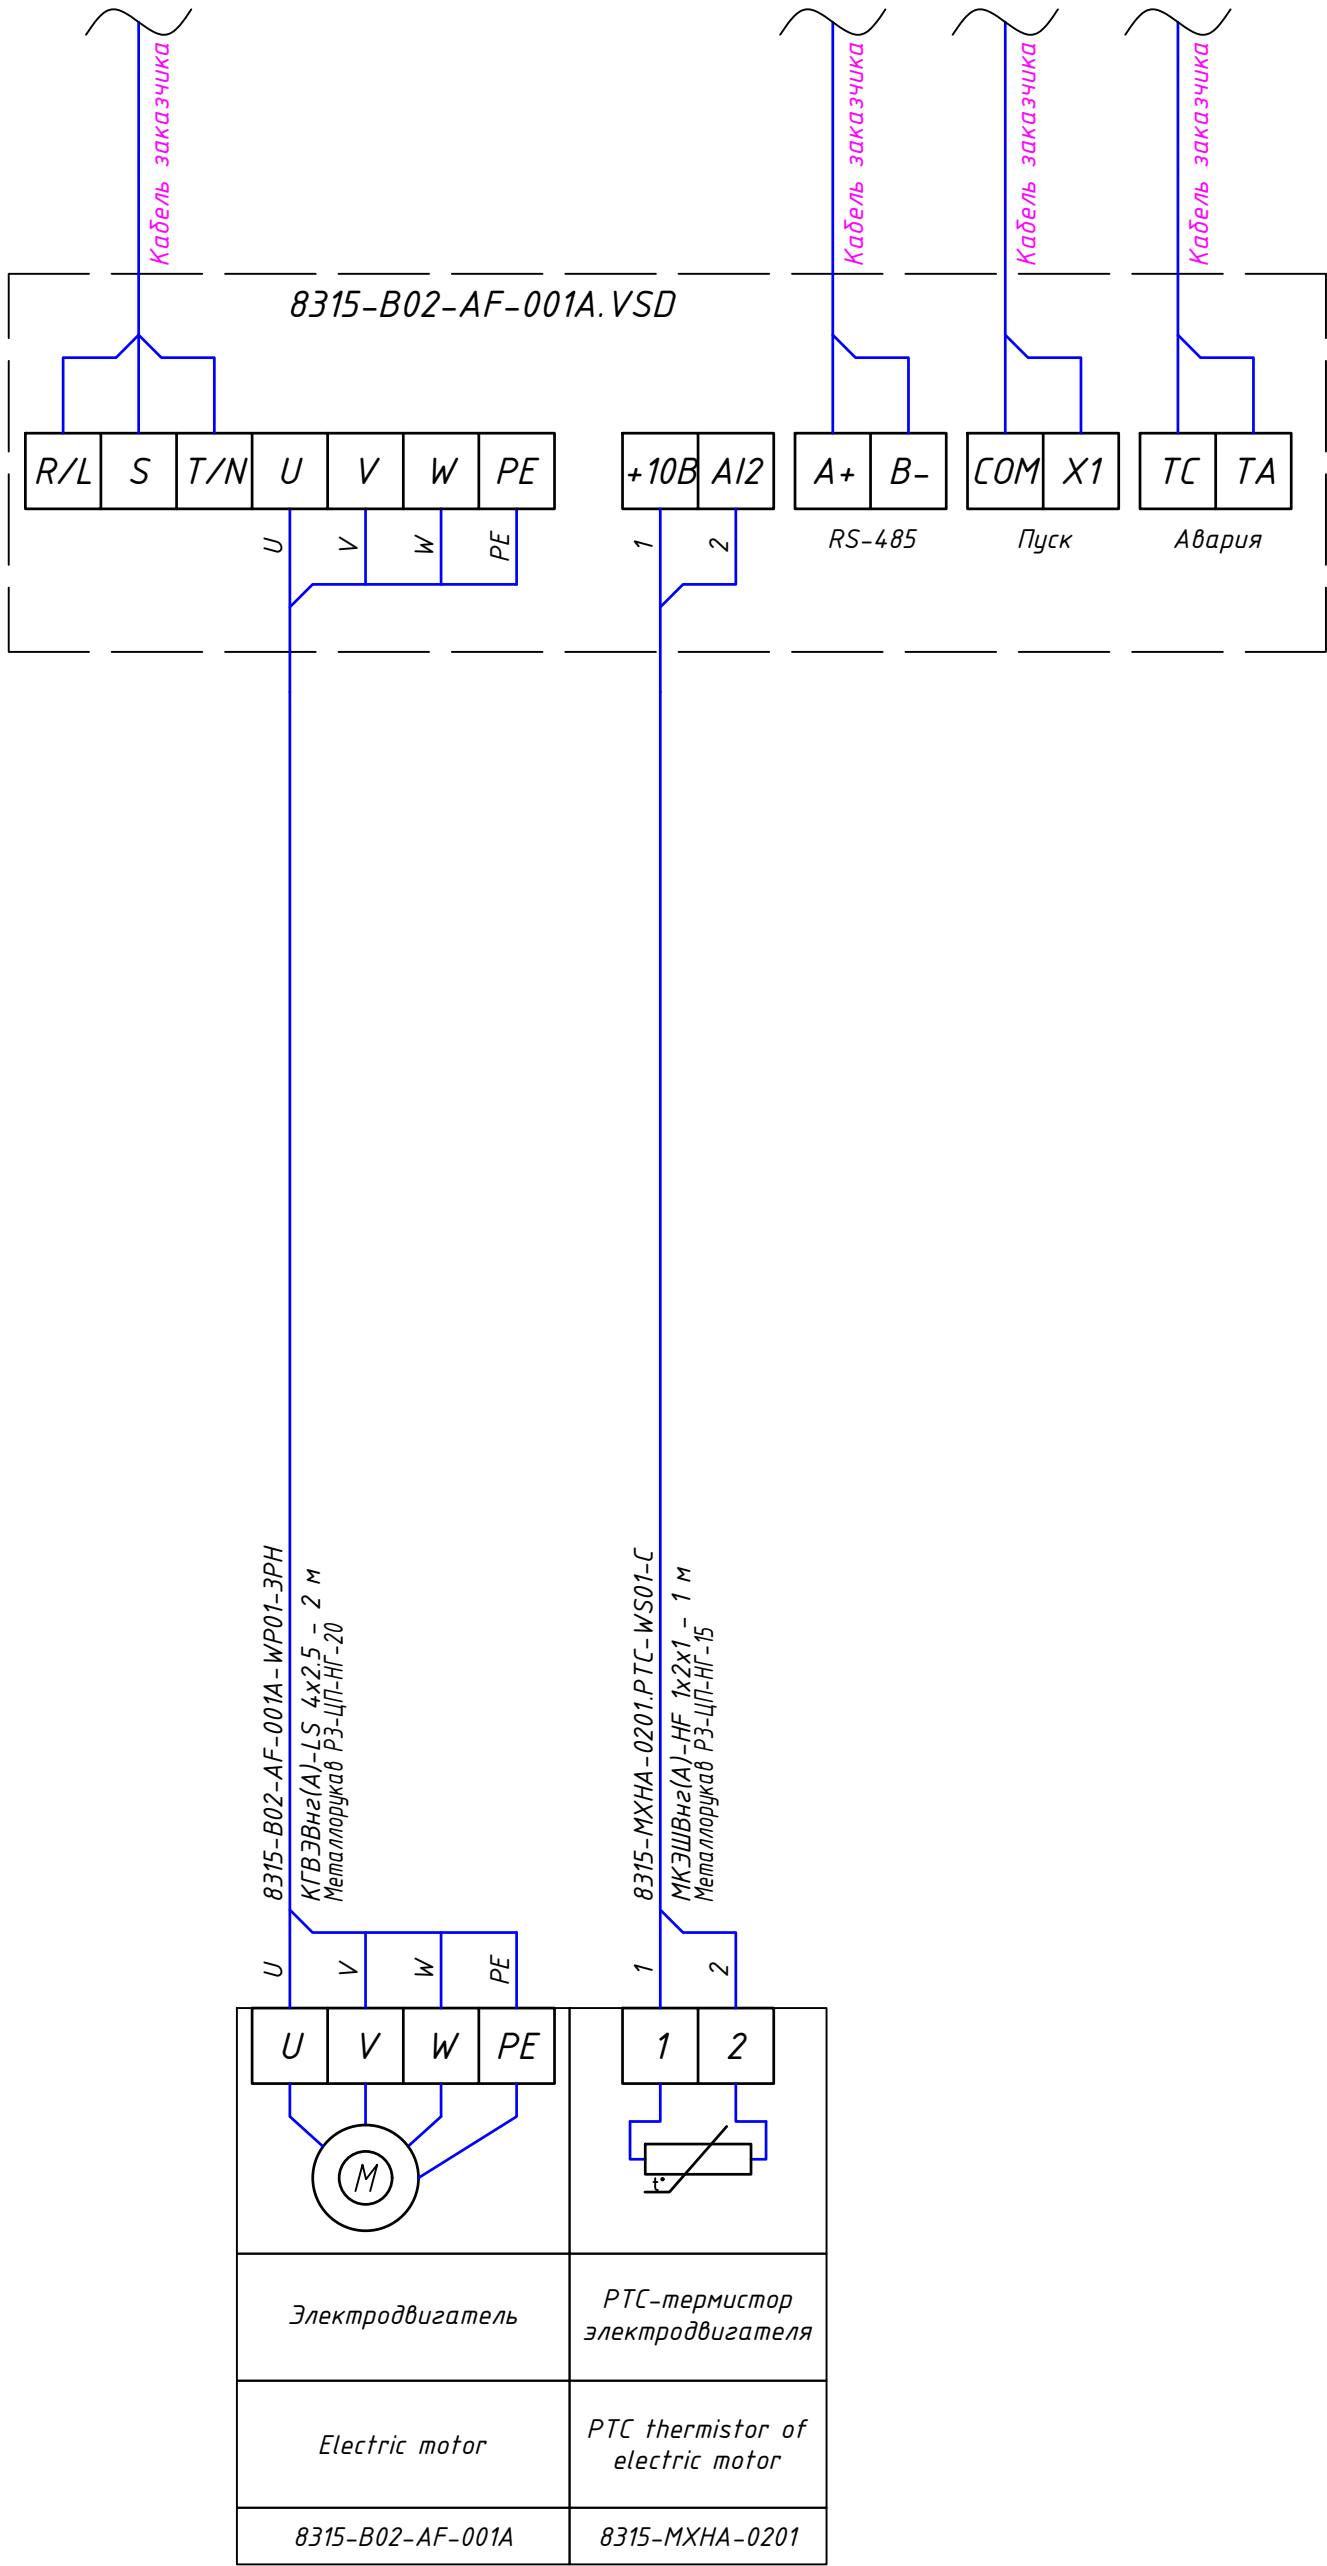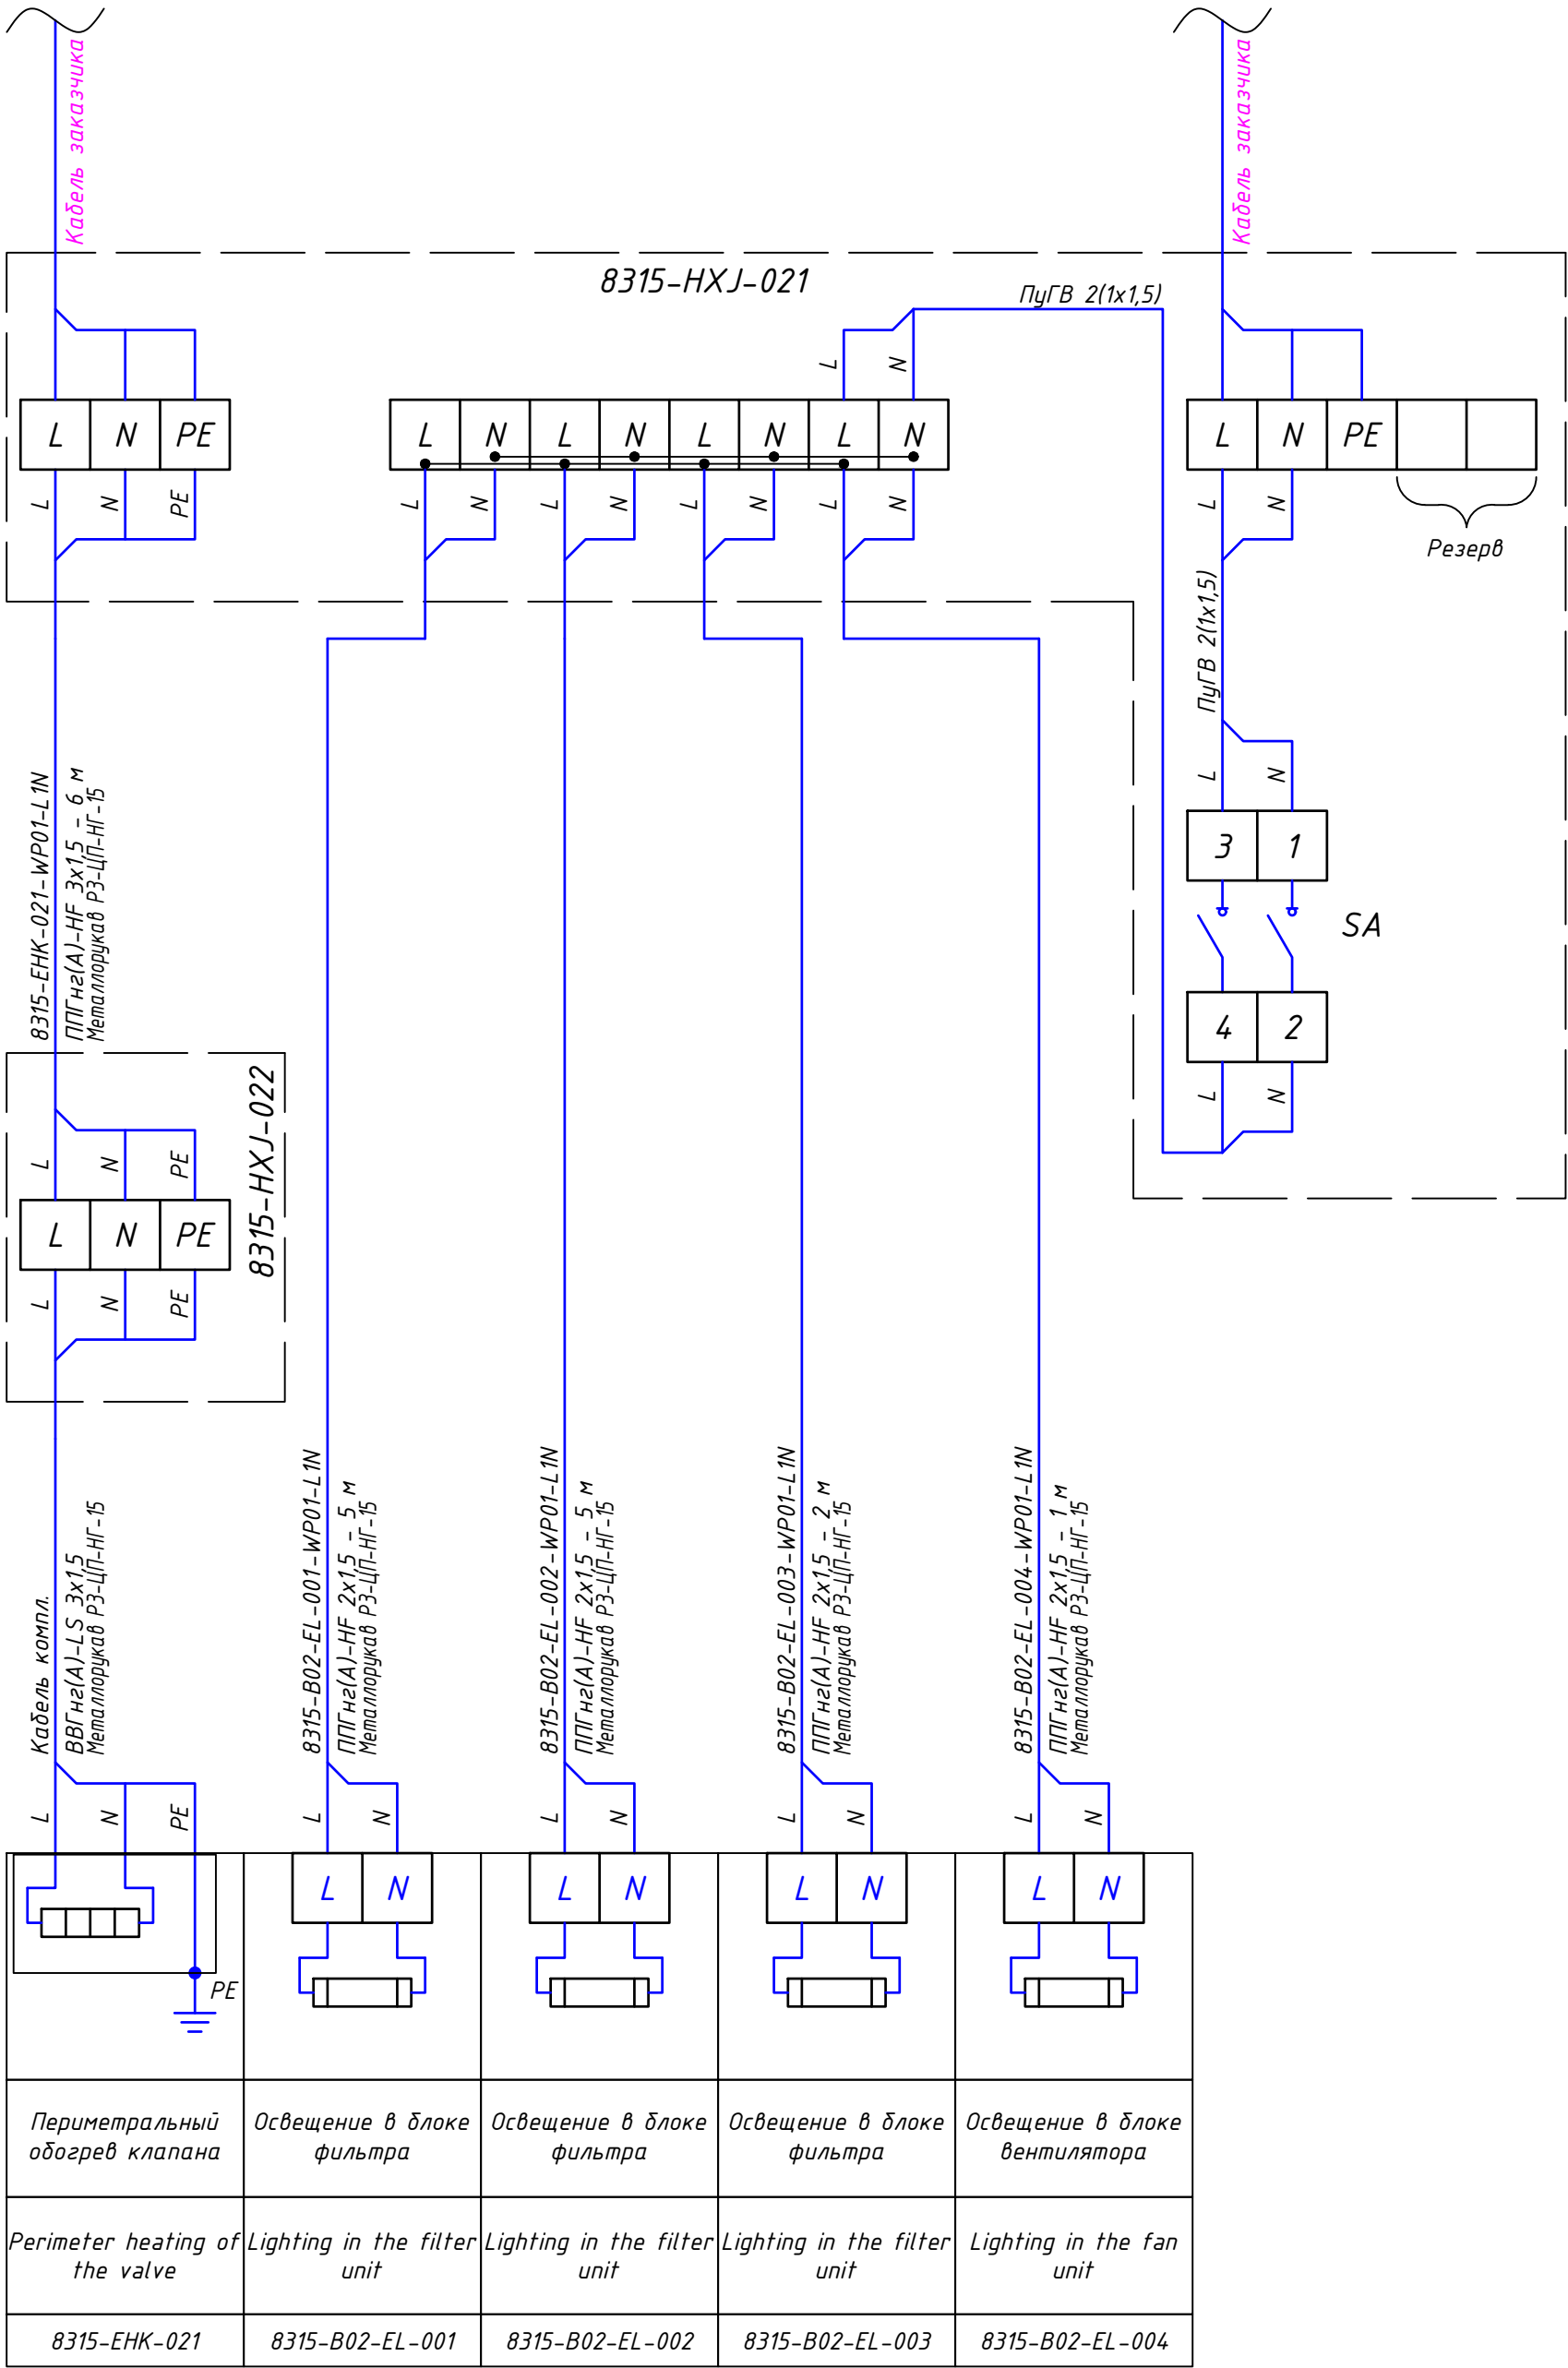


312	312	312	312	132	1234	12	12
Реле перепада давления на фильтре (ОВЕН РД30-ДД400)	Реле перепада давления на фильтре (ОВЕН РД30-ДД400)	Реле перепада давления на фильтре (ОВЕН РД30-ДД400)	Реле перепада давления на вентиляторе (ОВЕН РД30-ДД1000)	Термостат защиты от замораживания Т0 RGP TS-K3	Концевой выключатель	Канальный датчик температуры (Метран-276)	Датчик температуры обратной воды (Тесей ТСРТ-109)
Differential pressure switch on the filter (OVEN RD30-DD400)	Differential pressure switch on the filter (OVEN RD30-DD400)	Differential pressure switch on the filter (OVEN RD30-DD400)	Differential pressure switch on the fan (OVEN RD30-DD1000)	The thermostat protects against freezing RGP TS-K3	Limit switch	Channel temperature sensor (Metran-276)	Return water temperature sensor (Tesej TSPT-109)
8315-PDHS-4025	8315-PDHS-4026	8315-PDHS-4027	8315-PDHS-4028	8315-THS-6026	8315-ZHSC-0202	8315-THT-6027	8315-THT-6025



8315-PDHS-4025/01+ 8315-PDHS-4025/01- МКЭШВн2(A)-HF 1х2х1 - 5 м Металлоручкав РЗ-ЦП-НГ-15	8315-PDHS-4026/02+ 8315-PDHS-4026/02- МКЭШВн2(A)-HF 1х2х1 - 4 м Металлоручкав РЗ-ЦП-НГ-15	8315-PDHS-4027/03+ 8315-PDHS-4027/03- МКЭШВн2(A)-HF 1х2х1 - 1 м Металлоручкав РЗ-ЦП-НГ-15	8315-PDHS-4028/04+ 8315-PDHS-4028/04- МКЭШВн2(A)-HF 1х2х1 - 4 м Металлоручкав РЗ-ЦП-НГ-15	8315-THS-6026/05+ 8315-THS-6026/05- МКЭШВн2(A)-HF 1х2х1 - 5 м Металлоручкав РЗ-ЦП-НГ-15	8315-ZHSC-0202/06+ 8315-ZHSC-0202/06- МКЭШВн2(A)-HF 1х2х1 - 2 м Металлоручкав РЗ-ЦП-НГ-15	8315-THT-6027/07+ 8315-THT-6027/07- 8315-THT-6027/8315-HJB-506 Кабель заказчика Металлоручкав РЗ-ЦП-НГ-20	8315-THT-6025/08+ 8315-THT-6025/08- 8315-THT-6025/8315-HJB-506 Кабель заказчика Металлоручкав РЗ-ЦП-НГ-20
--	--	--	--	--	--	---	---

12	S1S2S3S4S5S6
Питание эл.привода на клапане (DA5FU24DS)	Концевые выключатели эл.привода на клапане (DA5FU24DS)
Power supply of the electric drive on the valve (DA5FU24DS)	Limit switches of the electric actuator on the valve (DA5FU24DS)
8315-B02-AX-001B	8315-B02-AX-001B

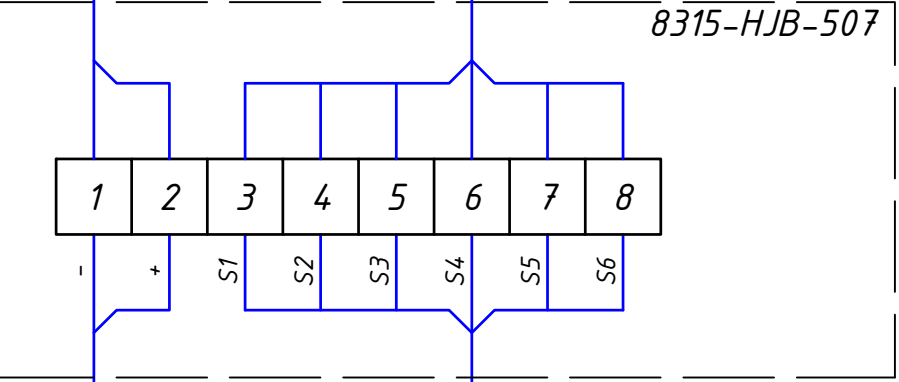



12	S1S2S3S4S5S6
Питание эл.привода на клапане (DA5FU24DS)	Концевые выключатели эл.привода на клапане (DA5FU24DS)
Power supply of the electric drive on the valve (DA5FU24DS)	Limit switches of the electric actuator on the valve (DA5FU24DS)
8315-B02-AX-002B	8315-B02-AX-002B

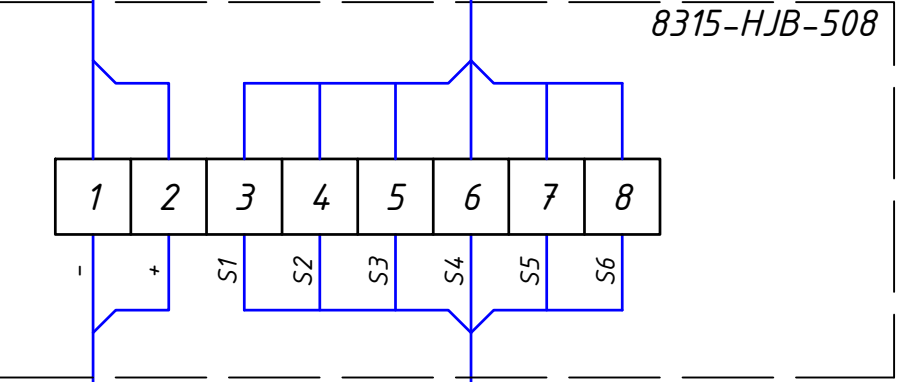

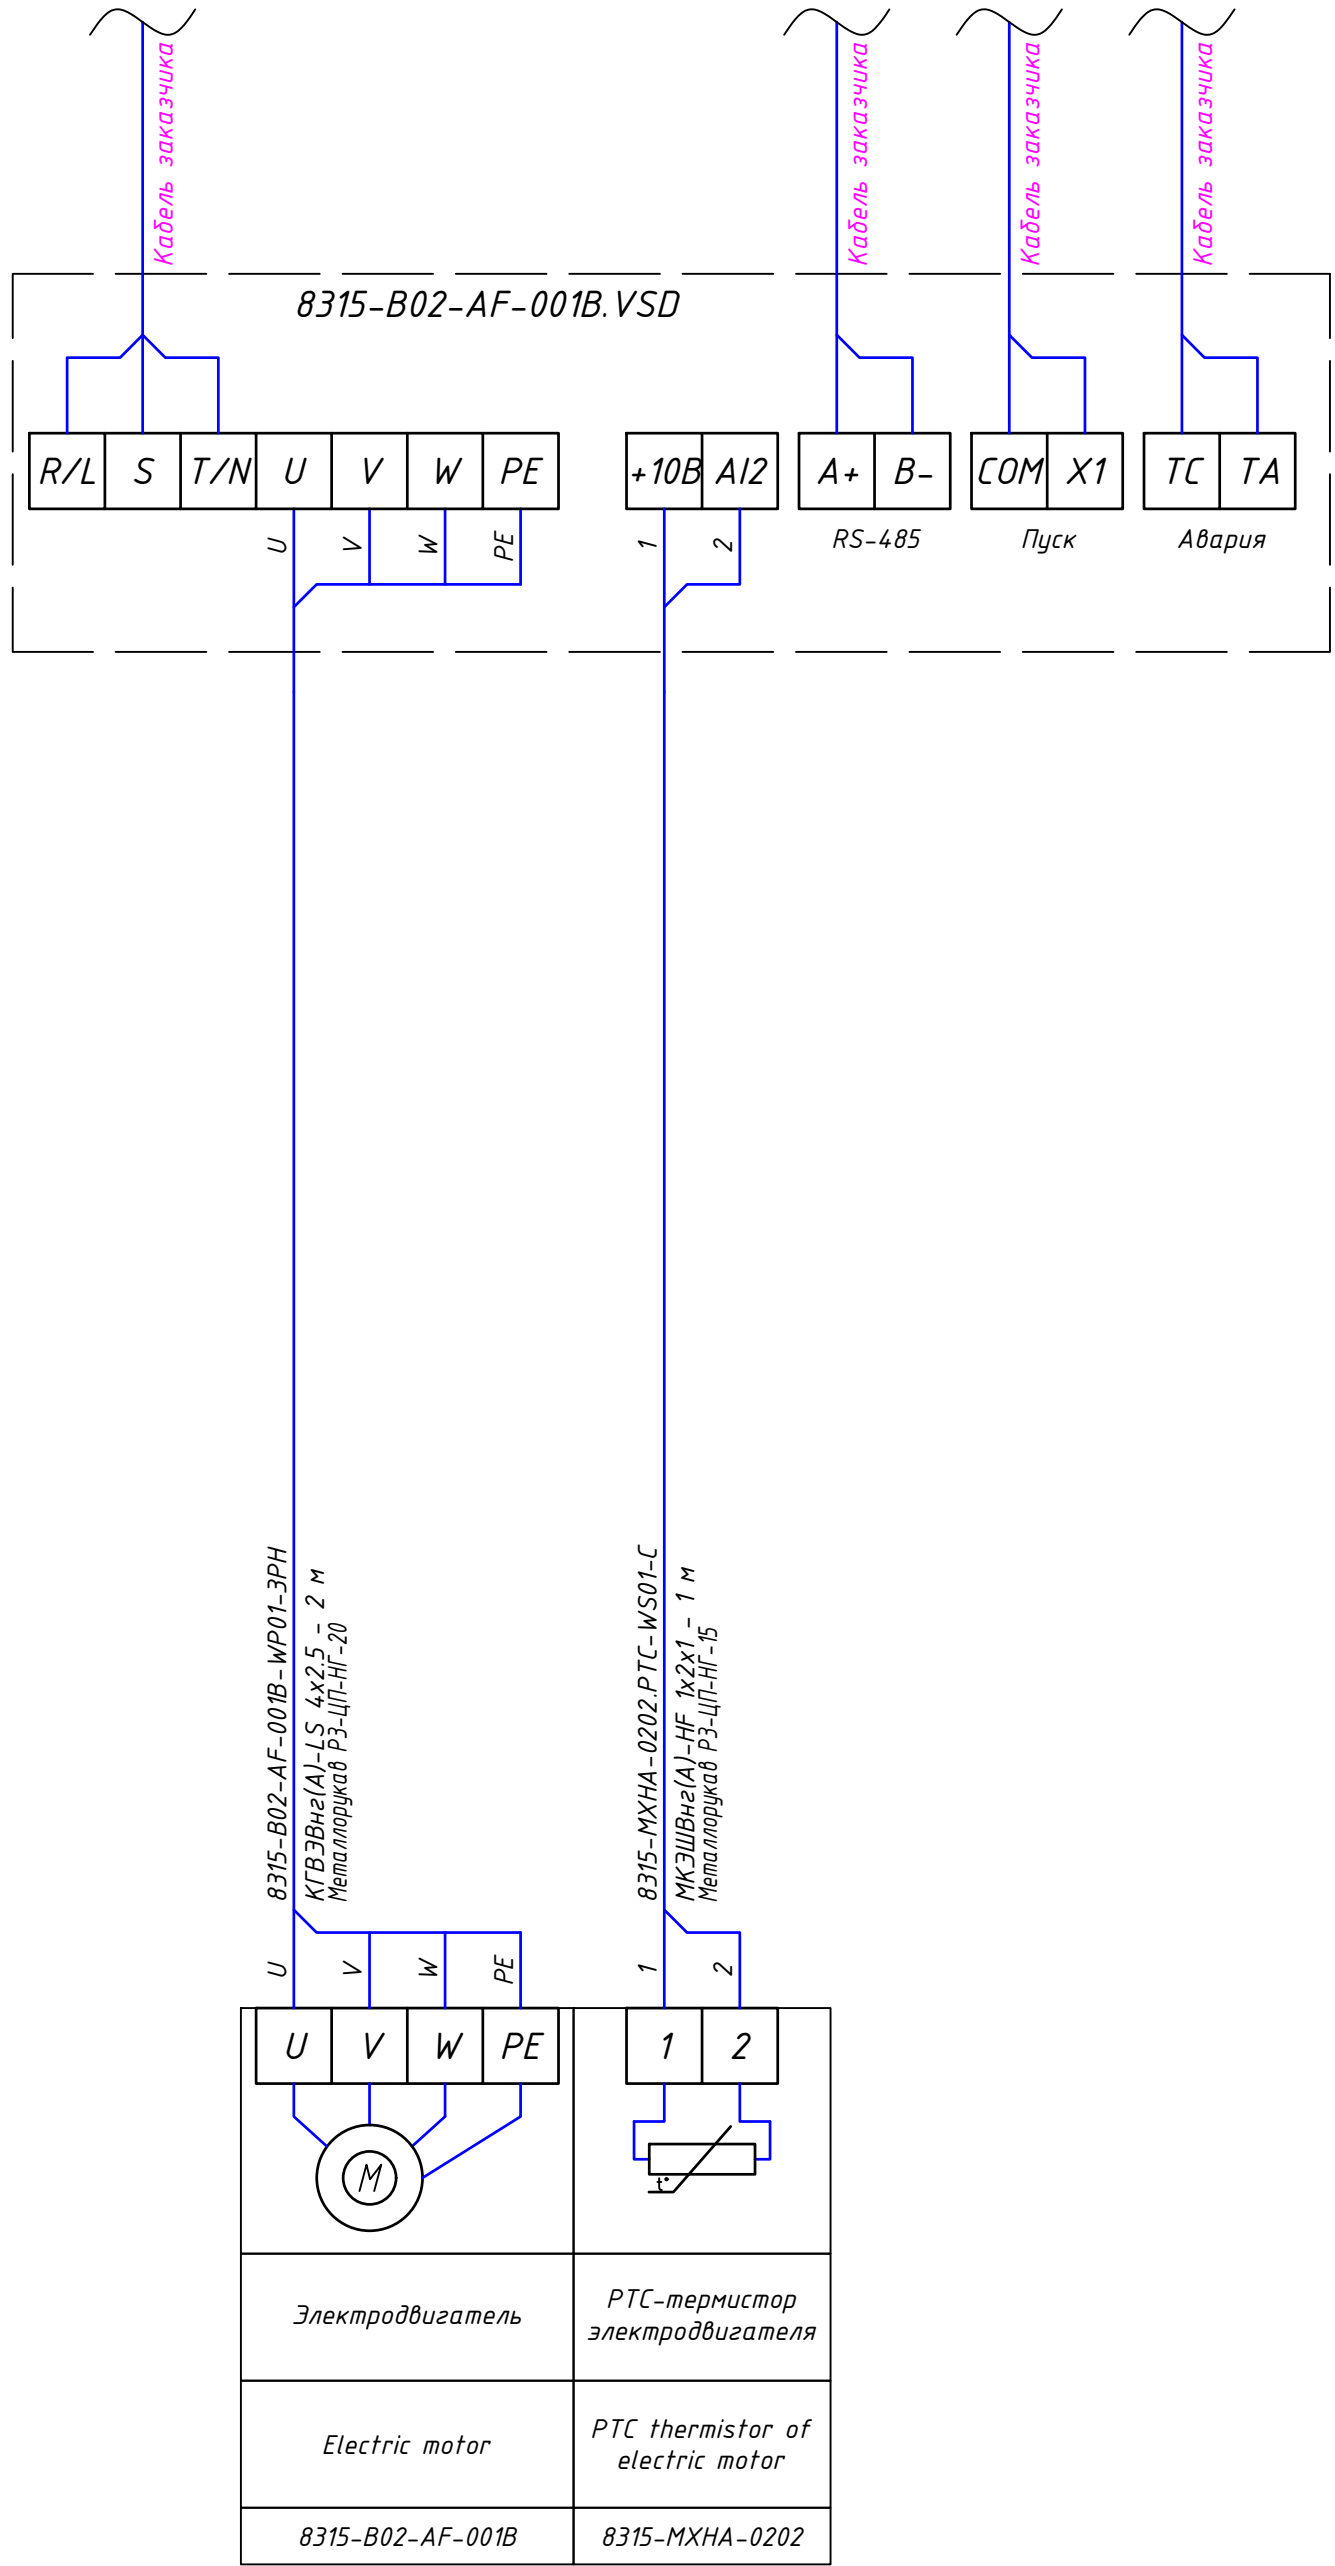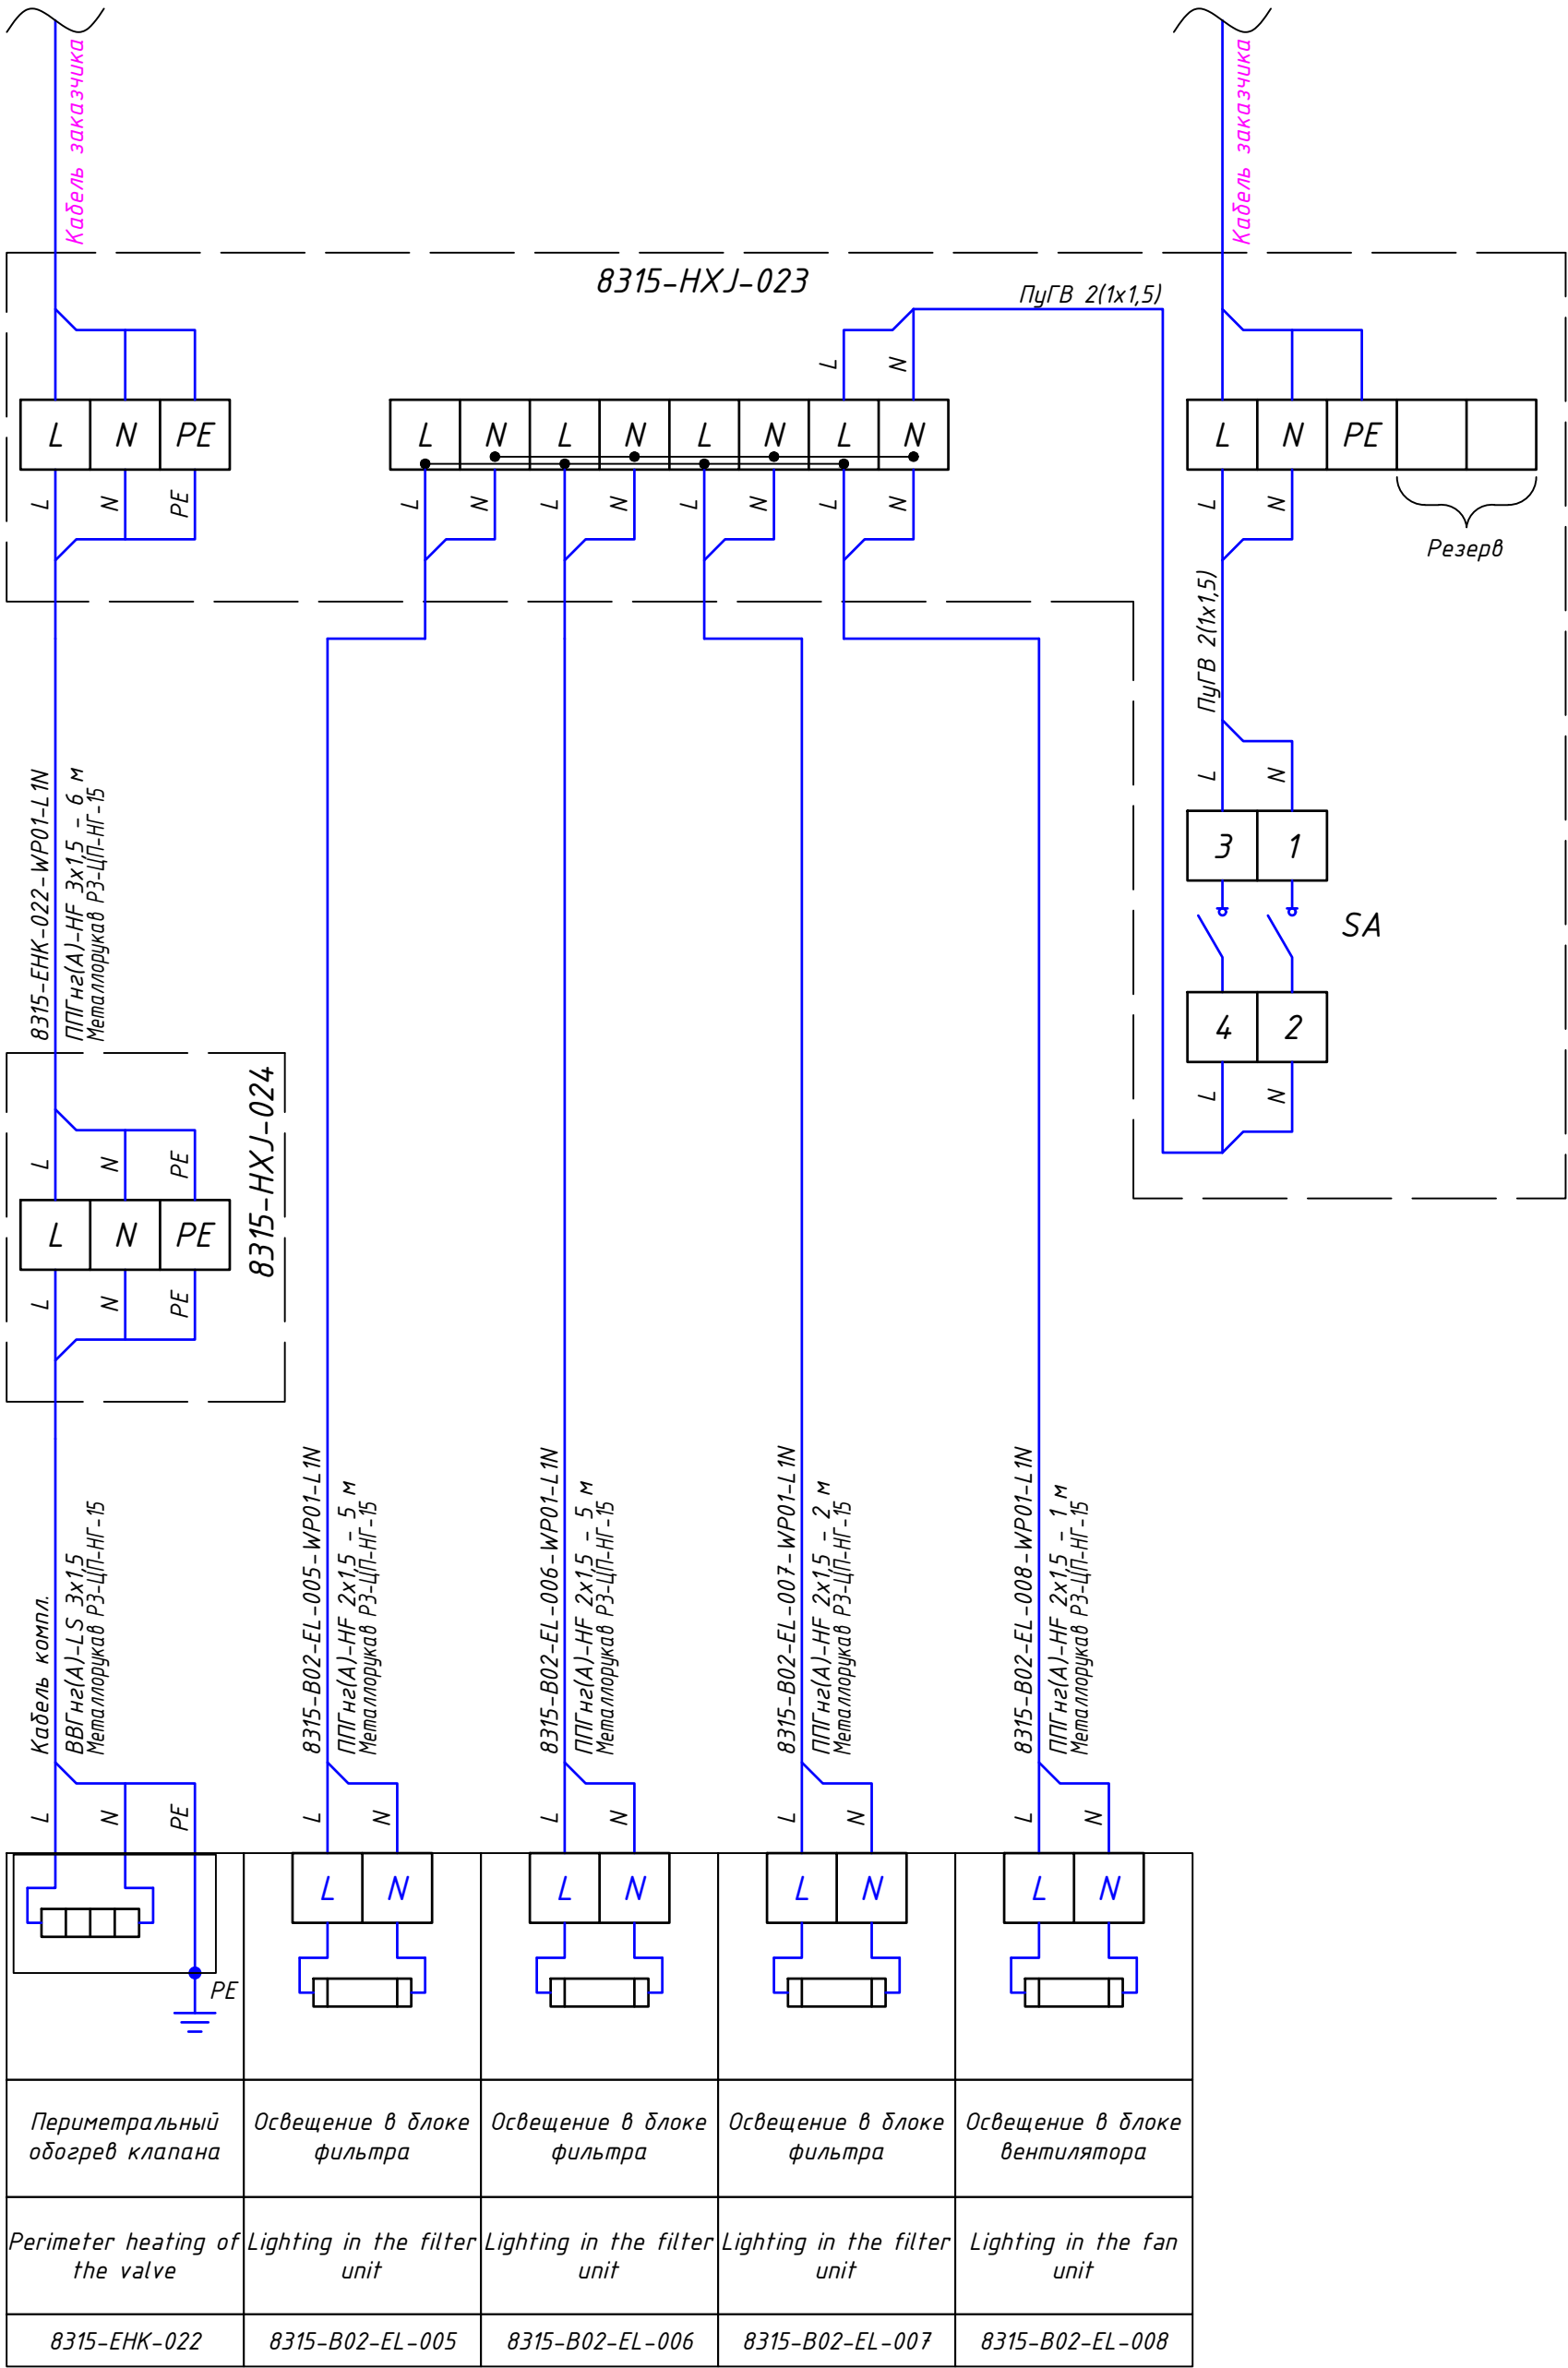

Поз.	Оборудование	Кол-во	БЗ
1	Преобразователь частоты VEDA VF-101-P5K5-0013-A-T4-C54-B-H (DBC00027) 5.5кВт, 13А, 380-480В, IP54	см. лист 2	24104,24112
	Каб. ввод под брониру. 20АК Ni ник. латунь ATELEX	1	Питание ЧРП
	Каб.ввод под металлорукав ВК-М25-16-МР20, IP67,ник.лат.	1	Питание ЭД
	Каб.ввод под металлорукав ВК-М20-12-МР15, IP67,ник.лат.	1	РТС-термистор
	Каб.ввод под металлорукав ВК-М20-16-МР20, IP67,ник.лат.	2	Modbus
	Каб.ввод под металлорукав ВК-М20-16-МР20, IP67,ник.лат.	1	Пуск/авария
	Шина РЕ, на изоляторах латунь ШНИ-6х9-6-У2-Ж,100А IEK	1	

БЗ-24104,24112
ЧРП - 3 шт(однотипные)

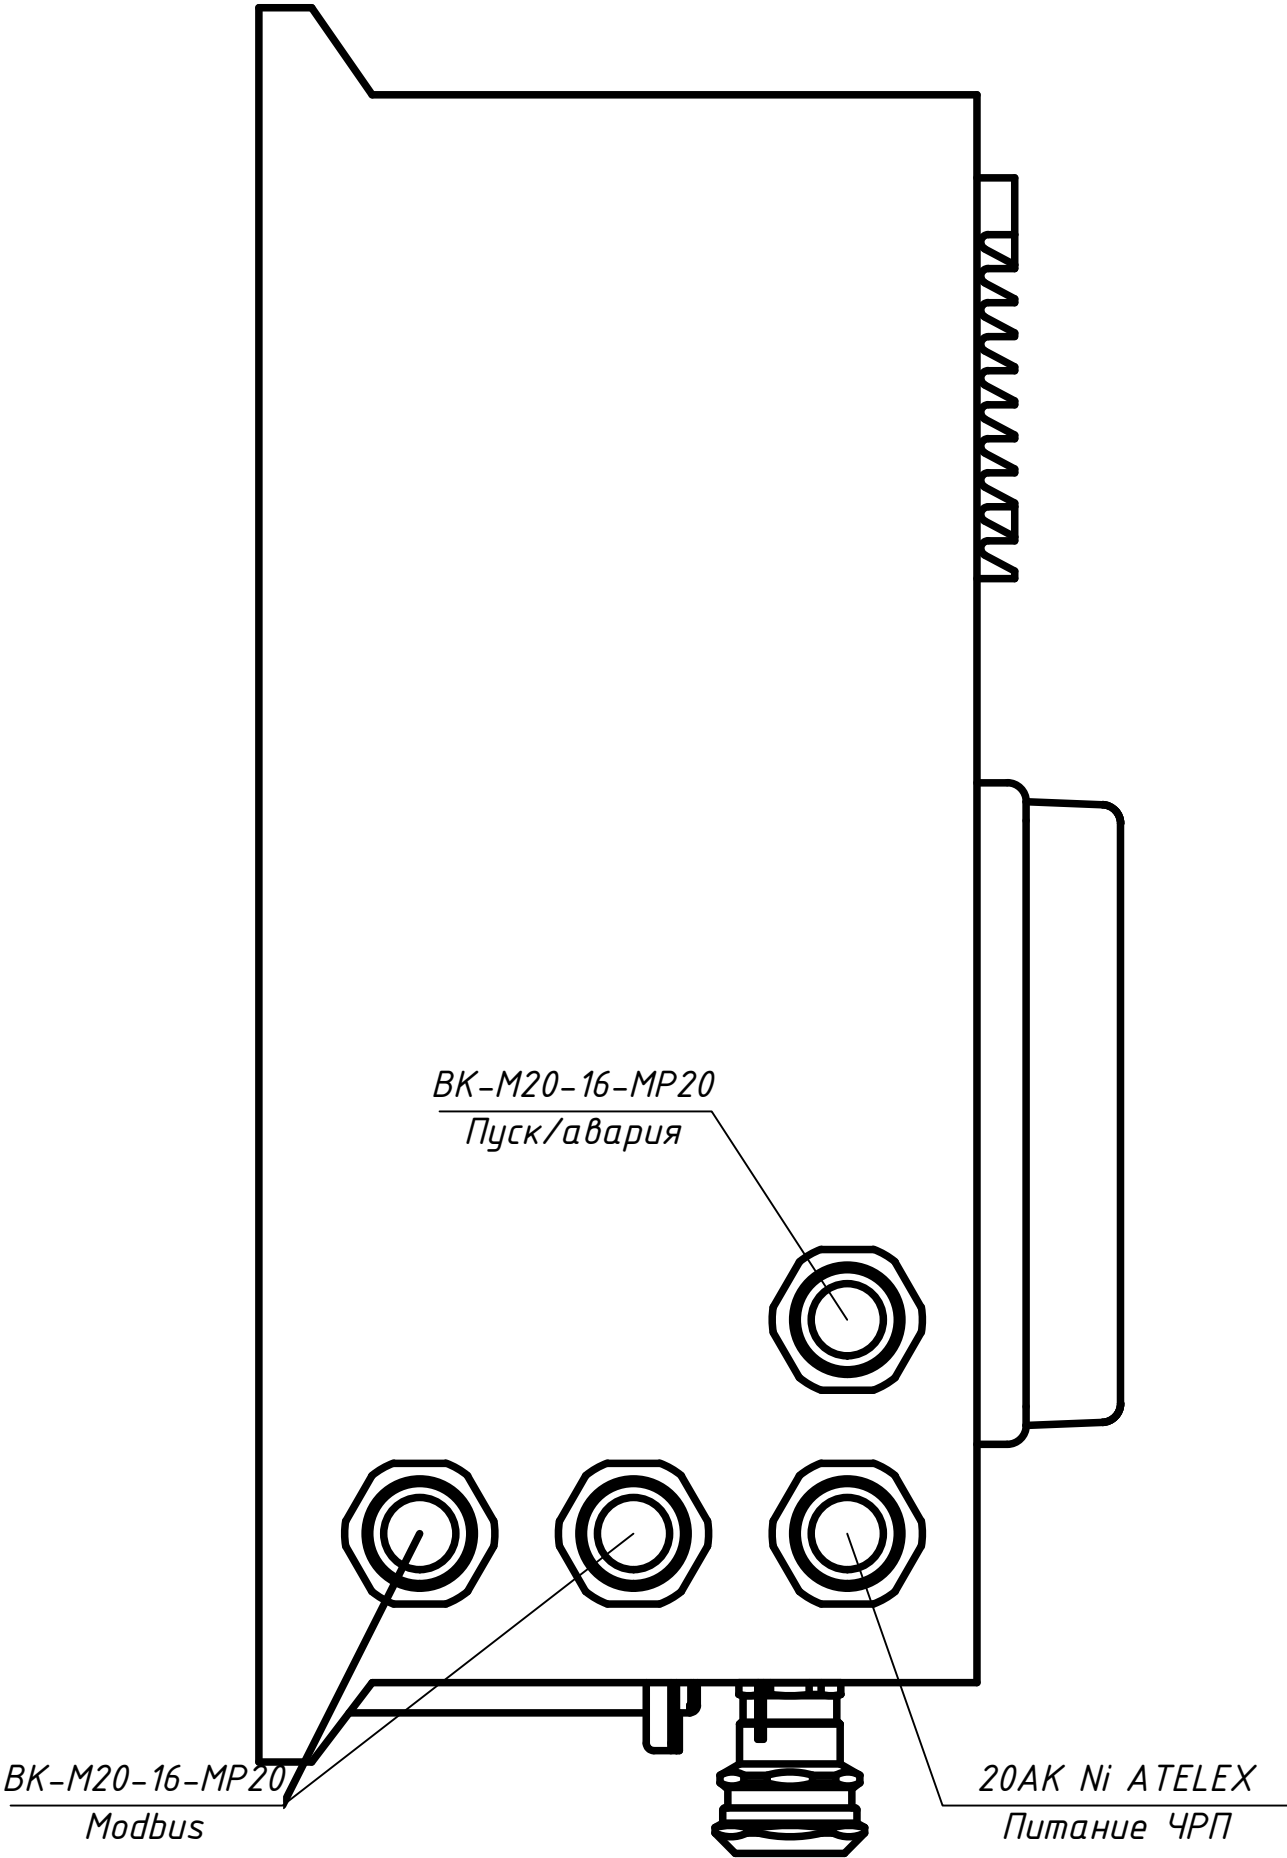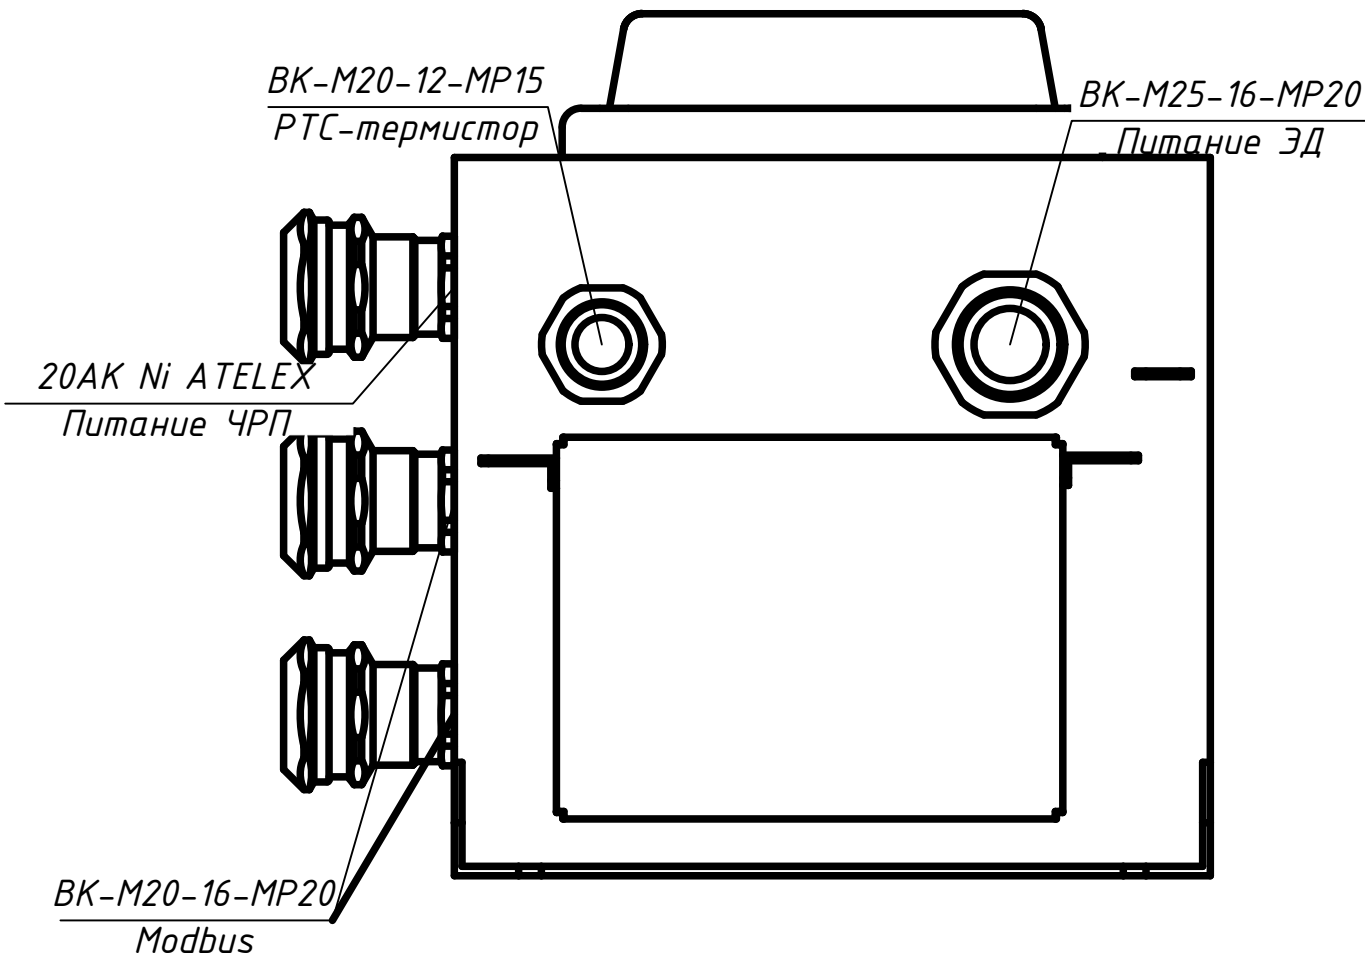

Инв. N подл.	Подпись и дата	Взам. инв. N

Изм.	Лист	Идокум.	Подп.	Дата	ВЦК "Сахара-С"-П-45 (δ/з 24104)	Лист
						10